



LANDSCAPE PLANT LIST

QTY	SYM	BOTANICAL NAME	COMMON NAME	SPECIFICATIONS
Trees				
15	CES	Conocarpus erectus sericeus	Silver Buttonwood	B&B, 10'ht. x 5'spr., 5'ct. 3" cal
8	LJ	Ligustrum japonicum	Southern Wax Privet	B&B, 10'ht. x 5'spr., 5'ct. 3" cal
7	QV	Quercus virginiana	Live Oak	B&B, 10'ht. x 5'spr., 5'ct. 3" cal
Shrubs				
168	CHR	Chrysobalanus icaco 'Red Tip'	Red Tip Cocoplum	3 gal., 24"ht. x 18"spr., 24" o.c.
143	CON	Conocarpus erectus	Green Buttonwood	3 gal., 24"ht. x 18"spr., 24" o.c.

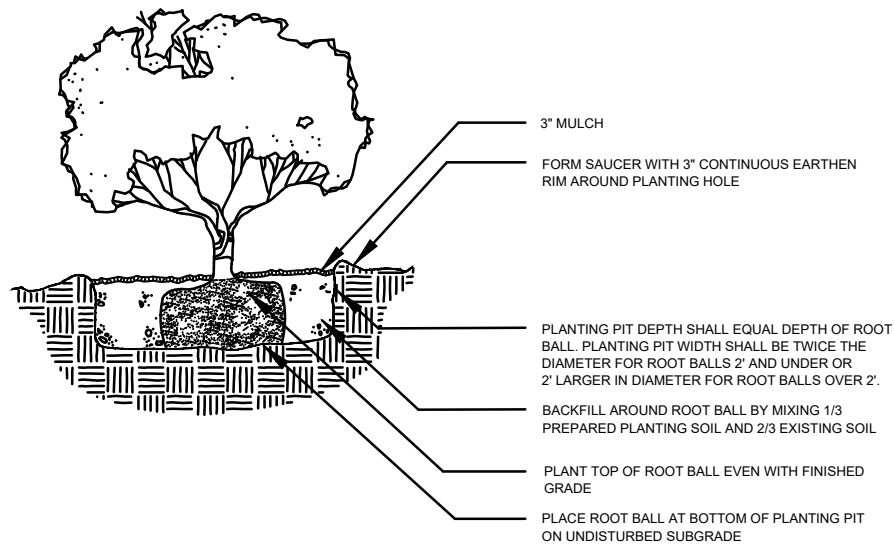

SHRUB/GROUNDCOVER PLANTING DETAIL


N.T.S.

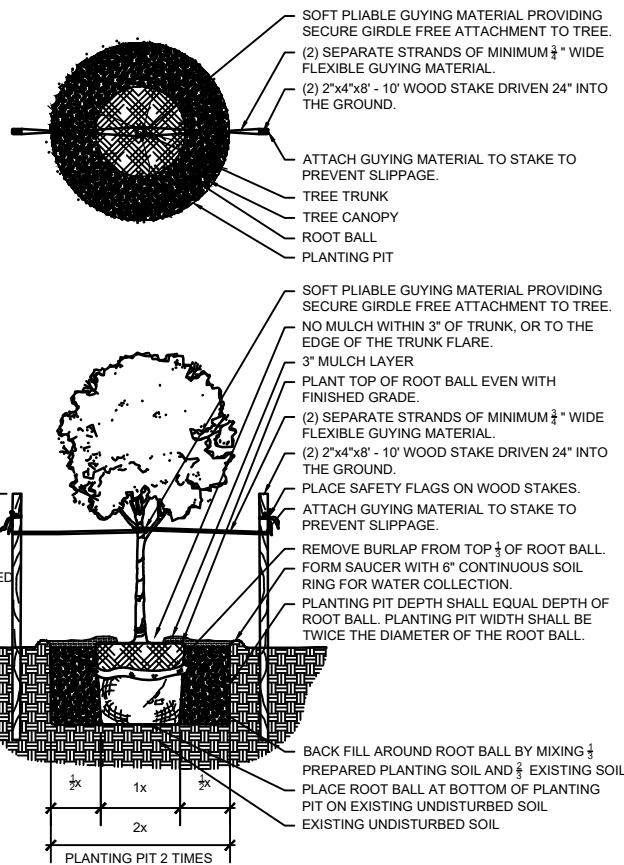

SMALL TREE PLANTING DETAIL

N.T.S.



FOR TREES UNDER 3" CALIPER

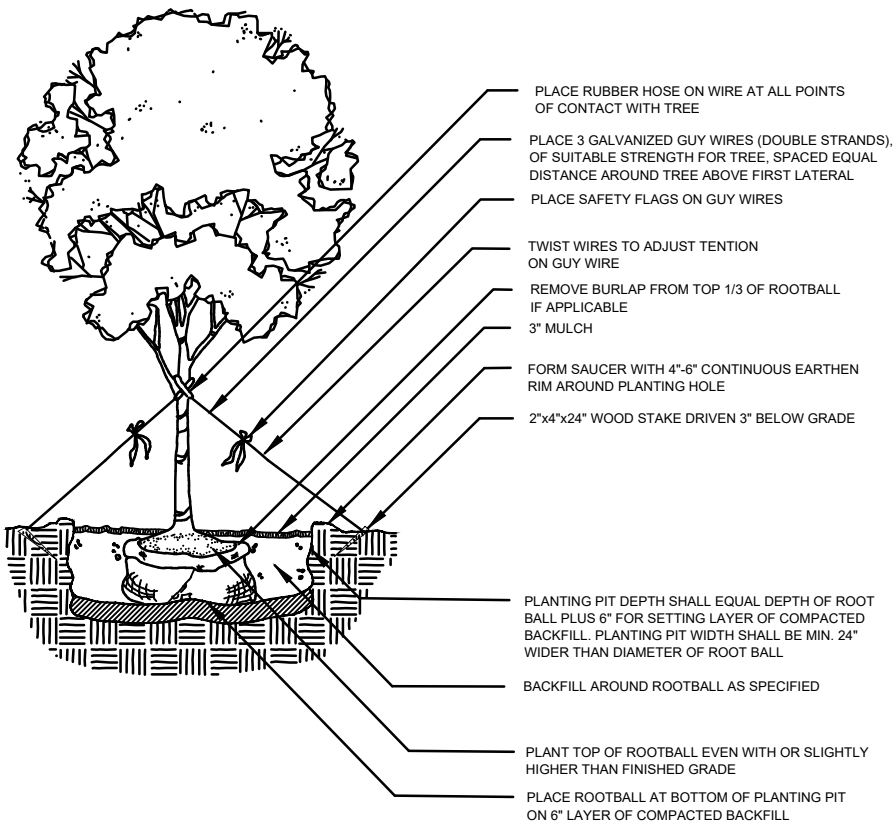

LARGE TREE PLANTING/GUY DETAIL

N.T.S.

FOR TREES 3" & OVER CALIPER

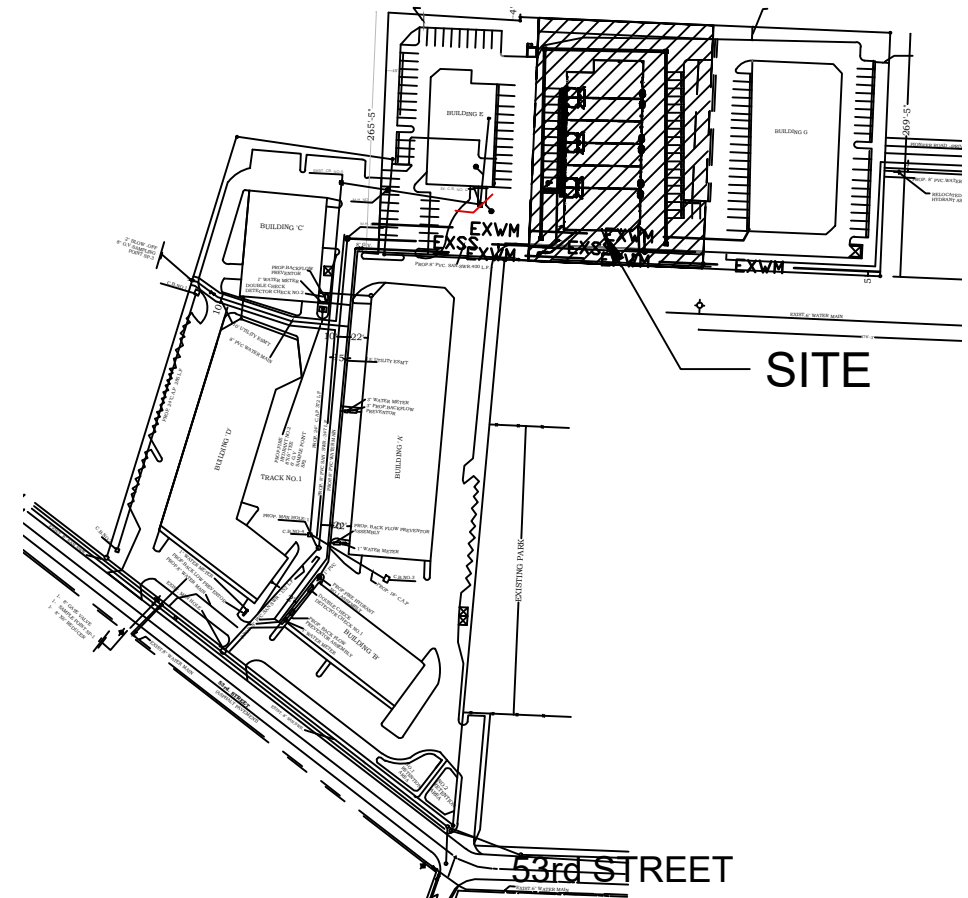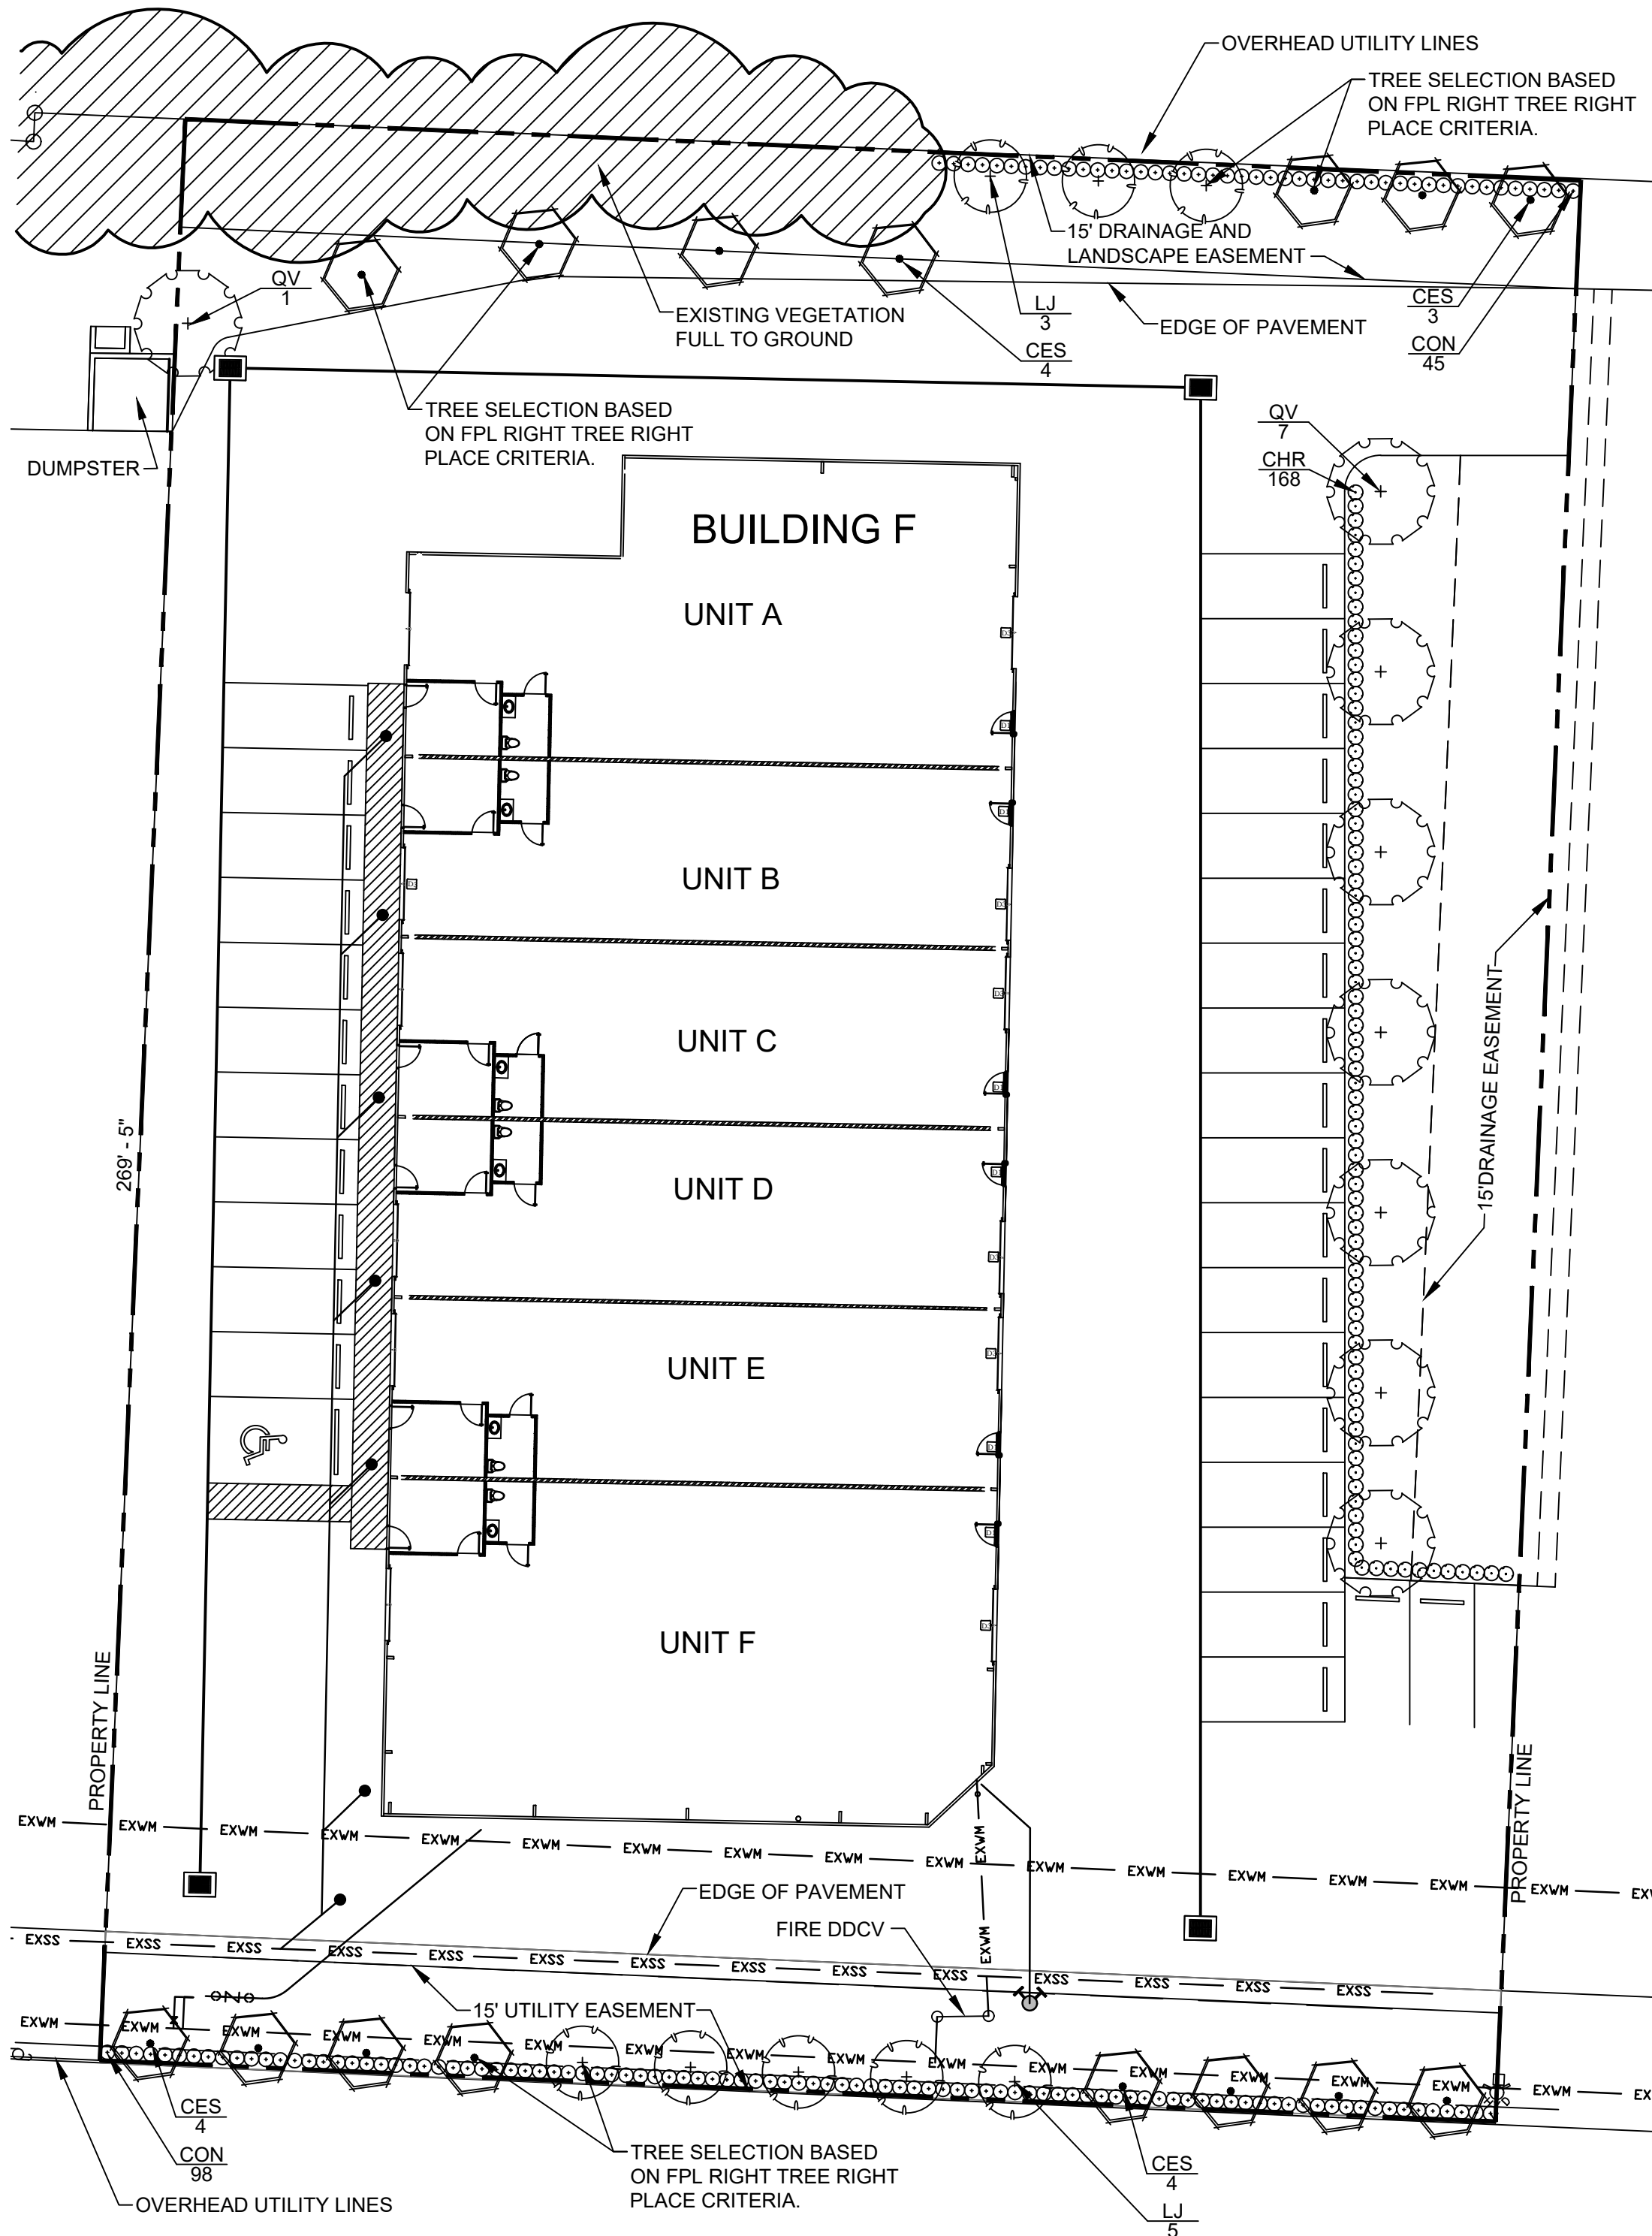

PROJECT NO.: 2101
DATE: 06/05/21
CAD FILE NAME: 2101LP-R0.DWG
XREF:
CAD PLOT DATE: 06/05/21

SUPERSEDED BY:
REVISION NO.:
DATE:



REVISIONS	DATE	BY	R#	DESCRIPTION
01/22	06/05/21	DAW	01	ADD WATER, SEWER, & DRAINAGE

© DAVID W. LOCKMILLER, PLA
THESE DRAWINGS ARE THE PROPERTY OF THE LANDSCAPE ARCHITECT AND ARE NOT TO BE USED FOR EXTENSIONS OR ON OTHER PROJECTS EXCEPT BY AGREEMENT IN WRITING WITH THE LANDSCAPE ARCHITECT.

1319 MANGONIA PARK WAREHOUSE
MANGONIA PARK, FLORIDA

LANDSCAPE PLAN

SHEET 1 OF 1

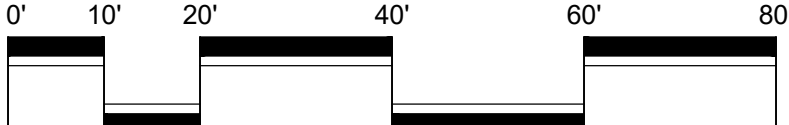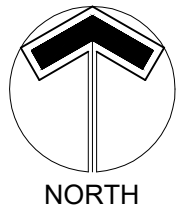

SCALE: 1" = 20'