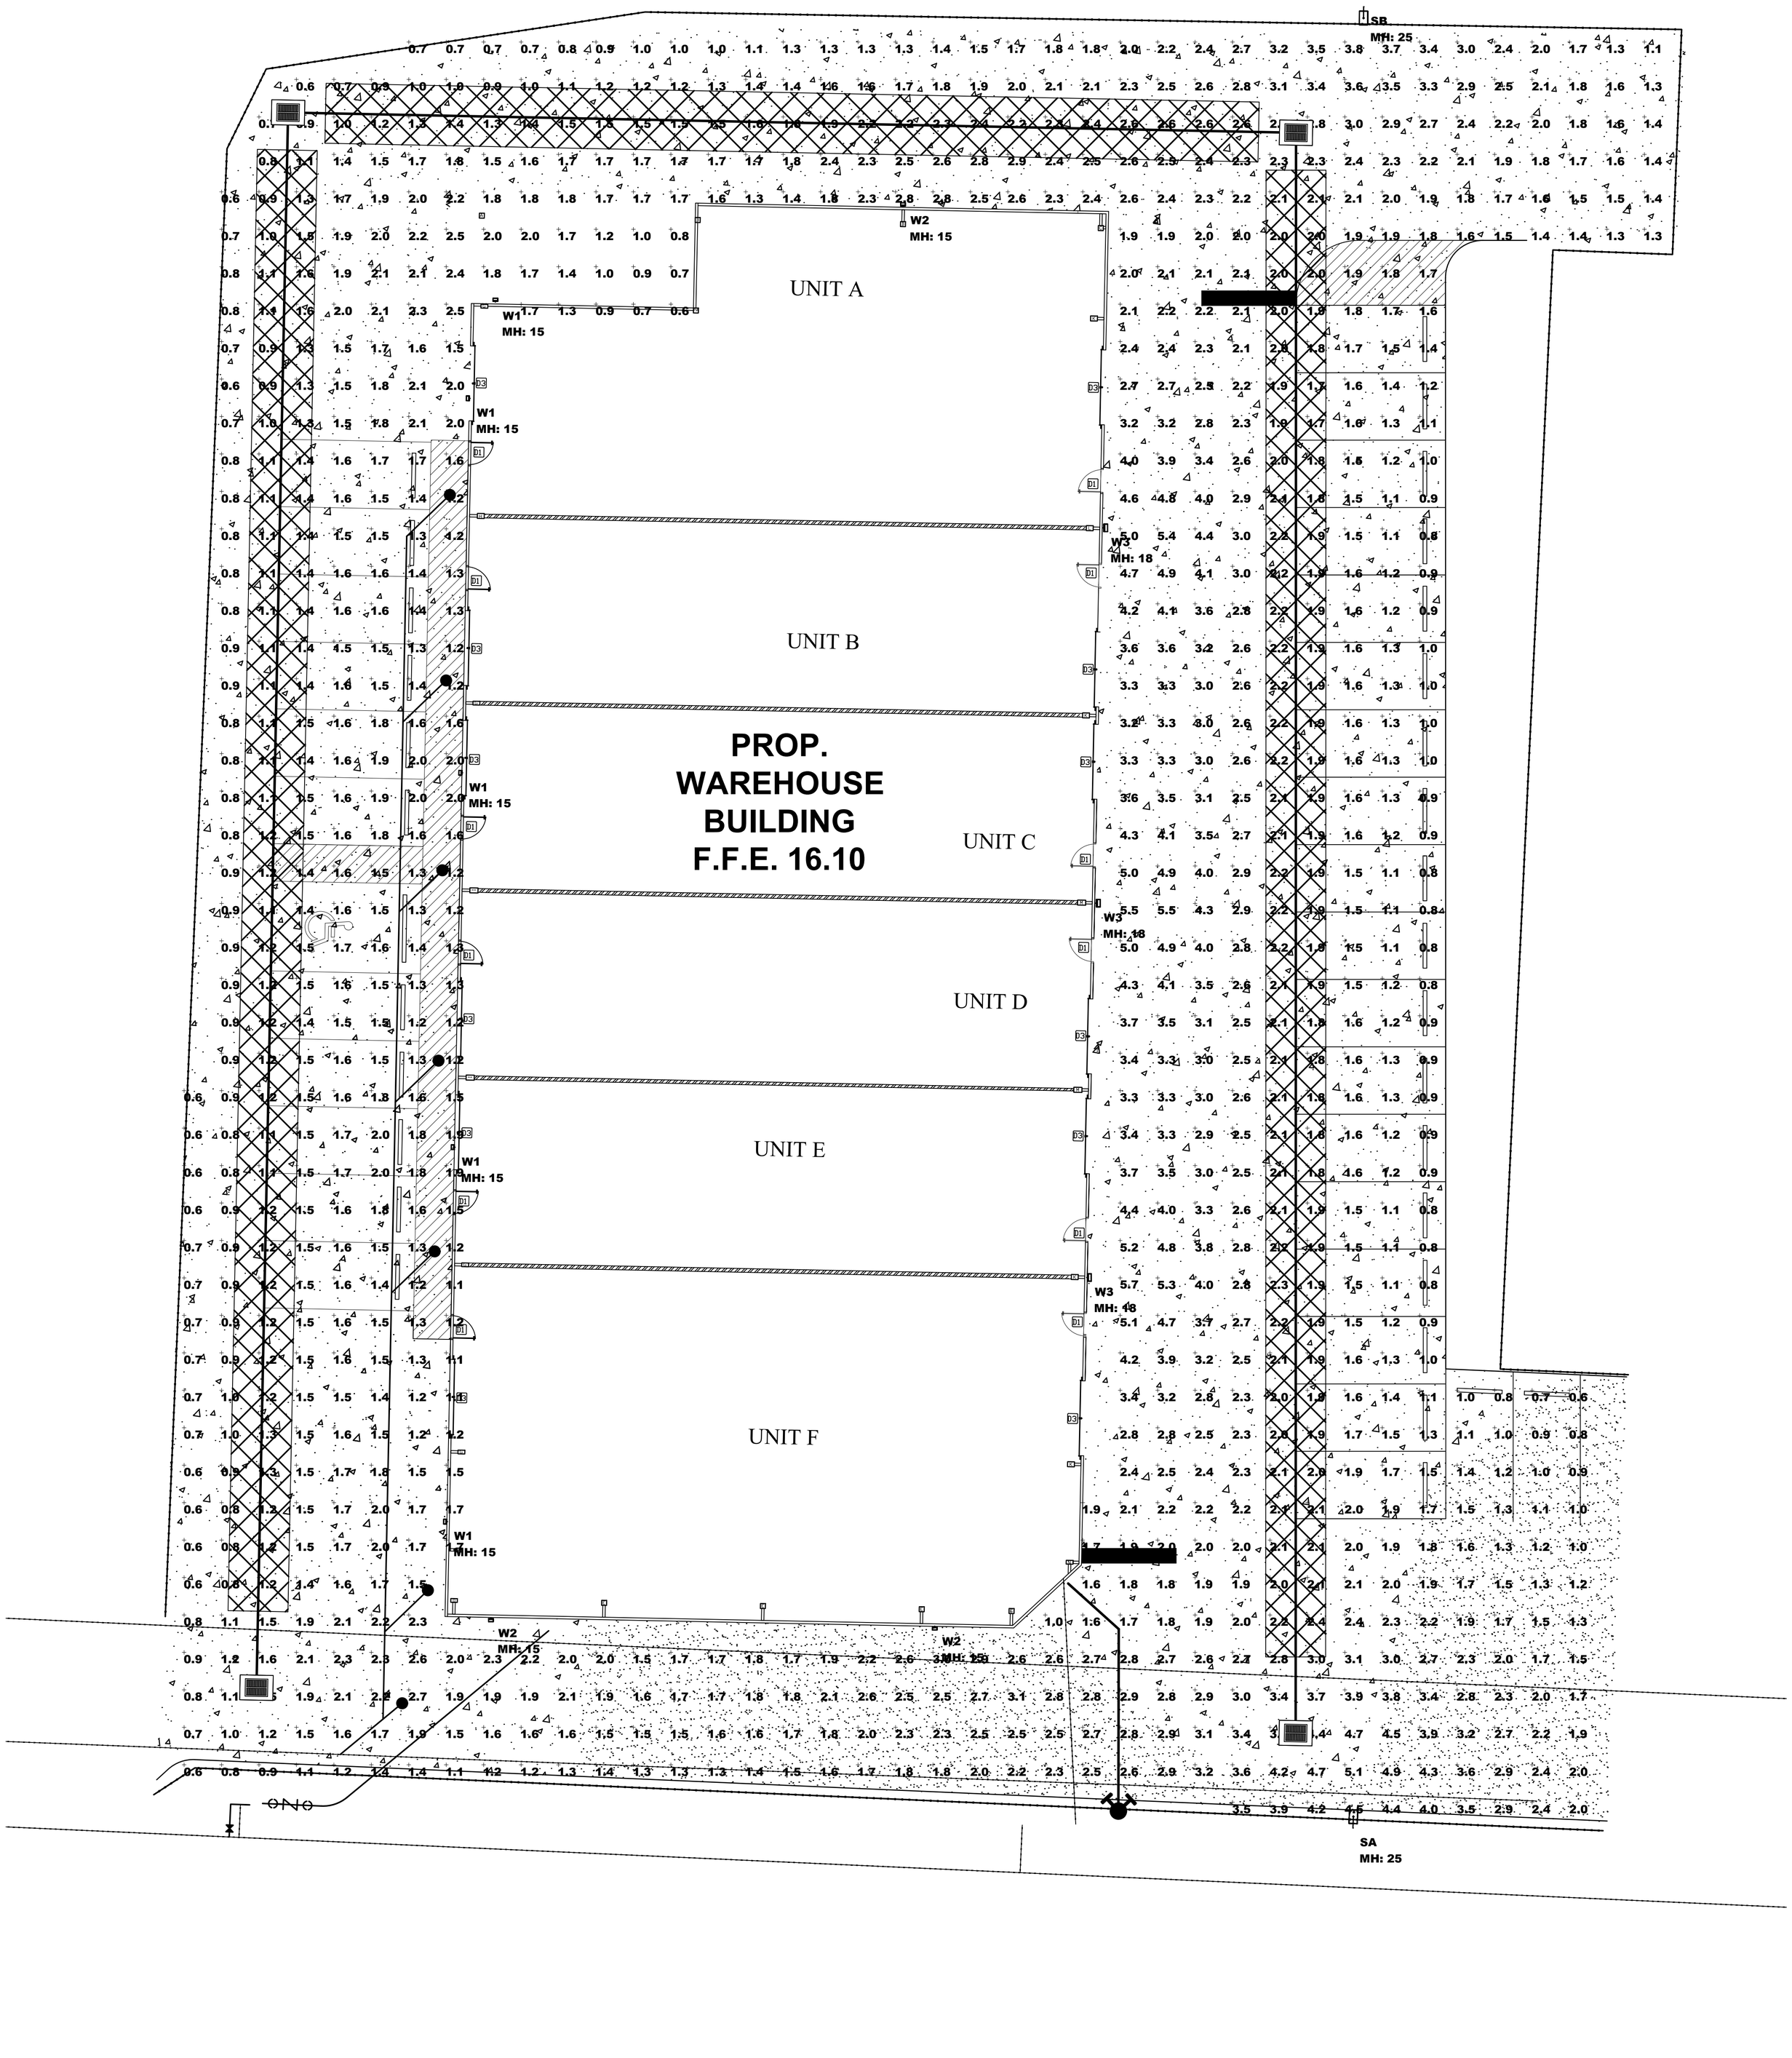


Luminaire Schedule: 1319 MANGONIA PARK WAREHOUSE - SITE_REV 1 MANGONIA PARK, FL 11/07/2024										
Symbol	**Qty**	**Label**	**Arrangement**	**Manufacturer**	**Description**	**Mounting**	**LLF**	**Lum Lumens**	**Lum Watts**	**Arrangement Watts**
	1	SA	Single	Lithonia Lighting	RSX1 LED P4 40K R4	POLE MOUNT A.F.G.	0.903	[redacted]	133.14	133.14
	1	SB	Single	Lithonia Lighting	RSX1 LED P3 40K R3	POLE MOUNT A.F.G.	0.903	[redacted]	109.44	109.44
	5	W1	Single	Lithonia Lighting	WDGE2 LED P4 40K 80CRI TFTM	WALL MOUNT A.F.F.	0.855	4202	46.6589	46.659
	3	W2	Single	Lithonia Lighting	WDGE2 LED P4 40K 80CRI T3M	WALL MOUNT A.F.F.	0.855	4268	46.6589	46.659
	3	W3	Single	Lithonia Lighting	WDGE3 LED P2 70CRI R4 40K	WALL MOUNT A.F.F.	0.855	8779	59.2761	59.276

Calculation Summary: 1319 MANGONIA PARK WAREHOUSE - SITE_REV 1 MANGONIA PARK, FL 11/07/2024										
Label	**Calc Type**	**Units**	**Spacing L-R (FT)**	**Spacing T-B (FT)**	**Height (FT)**	**Avg**	**Max**	**Min**	**Avg/Min**	**Max/Min**
PARKING & DRIVE LANES	Illuminance	Fc	5	5	0	1.93	5.7	0.6	3.22	9.50