



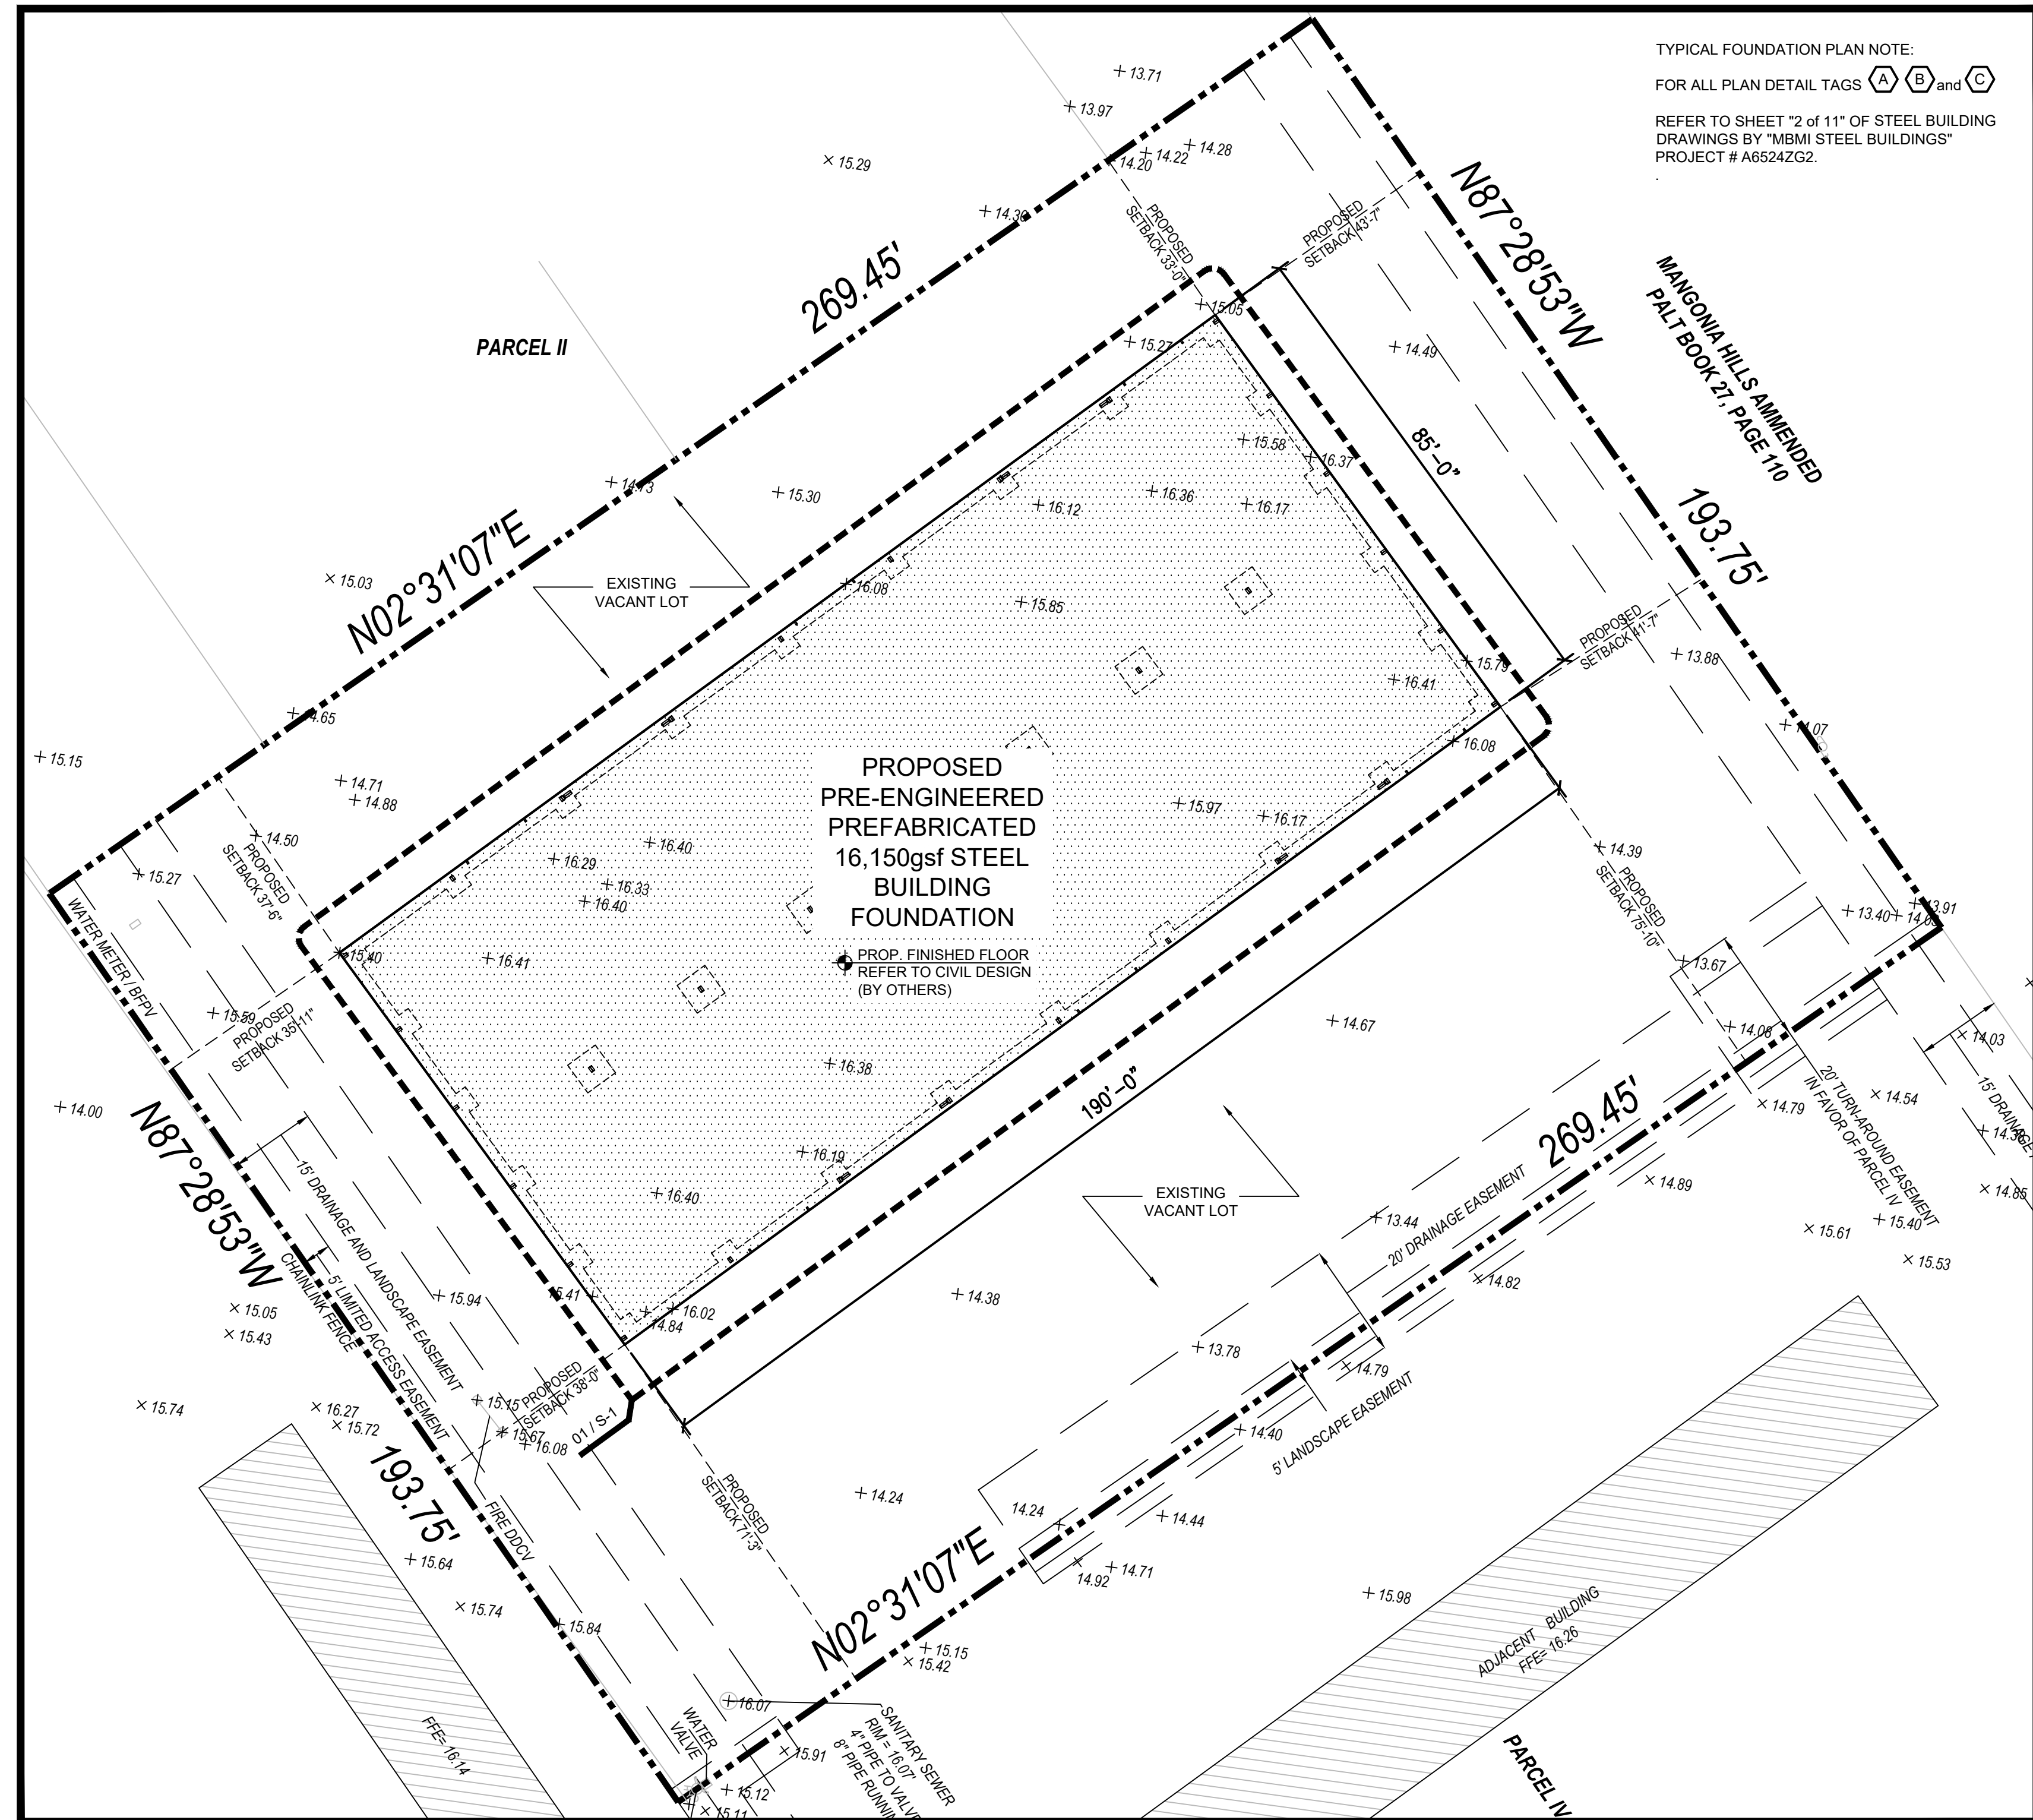

THE SCOPE OF WORK FOR THIS PROJECT CONSISTS EXCLUSIVELY OF THE STRUCTURAL FOUNDATION DESIGN FOR A PRE-ENGINEERED, PREFABRICATED 85' x 190' METAL BUILDING TO BE CONSTRUCTED ON A VACANT LOT. REFER TO DRAWINGS BY "MBMI STEEL BUILDINGS" 4723 W. ATLANTIC AVE., SUITE A20, DELRAY BEACH FOR ANY/ALL INFORMATION IN REGARDS TO THE METAL BUILDING. PROJ. #A6524ZG2.

1. CONTRACTOR IS RESPONSIBLE FOR MEANS AND METHODS OF CONSTRUCTION AND TO ENSURE PROPERITY OF WORK. ANY CHANGES ARE APPLIED UNTIL DRAWS SET STRUCTURAL WORK OUTLINED IN THIS PROPOSED SET IS COMPLETED.
2. ALL MATERIALS AND WORKSMANSHIP SHALL BE IN ACCORDANCE WITH THE 2023 FLORIDA BUILDING CODE (8TH EDITION).
3. ANY CHANGES TO THE FOUNDATION DESIGN CONTAINED HEREIN THESE DRAWINGS SHALL HAVE BEEN REVIEWED AND APPROVED IN WRITING BY THE STRUCTURAL ENGINEER PRIOR TO COMMENCING WORK ON ITEMS AFFECTED.
4. CONTACT ENGINEER WITH ANY QUESTIONS OR DISCREPANCIES FOUND ON DRAWINGS, IF ANY
5. CONTRACTOR TO VISIT SITE AND SHALL VERIFY ALL EXISTING DIMENSIONS, CLEARANCES, ELEVATIONS, SUBSTRATES AND CONDITIONS PRIOR TO BEGINNING CONSTRUCTION.
6. THE WORK DEFINED WITHIN THIS DRAWINGS SET IS INTENDED TO ADDRESS THE STRUCTURAL FOUNDATION DESIGN FOR A PRE-ENGINEERED, PREFABRICATED 65' X 190' METAL BUILDING BY "MMB STEEL BUILDINGS" PROJECT # 86502402.
7. PROVIDE NEOPRENE PADS OR 90# FELL PAPER BENEATH BOTTOM OF ALL STEEL BASE PLATES AND CONCRETE, TYP.

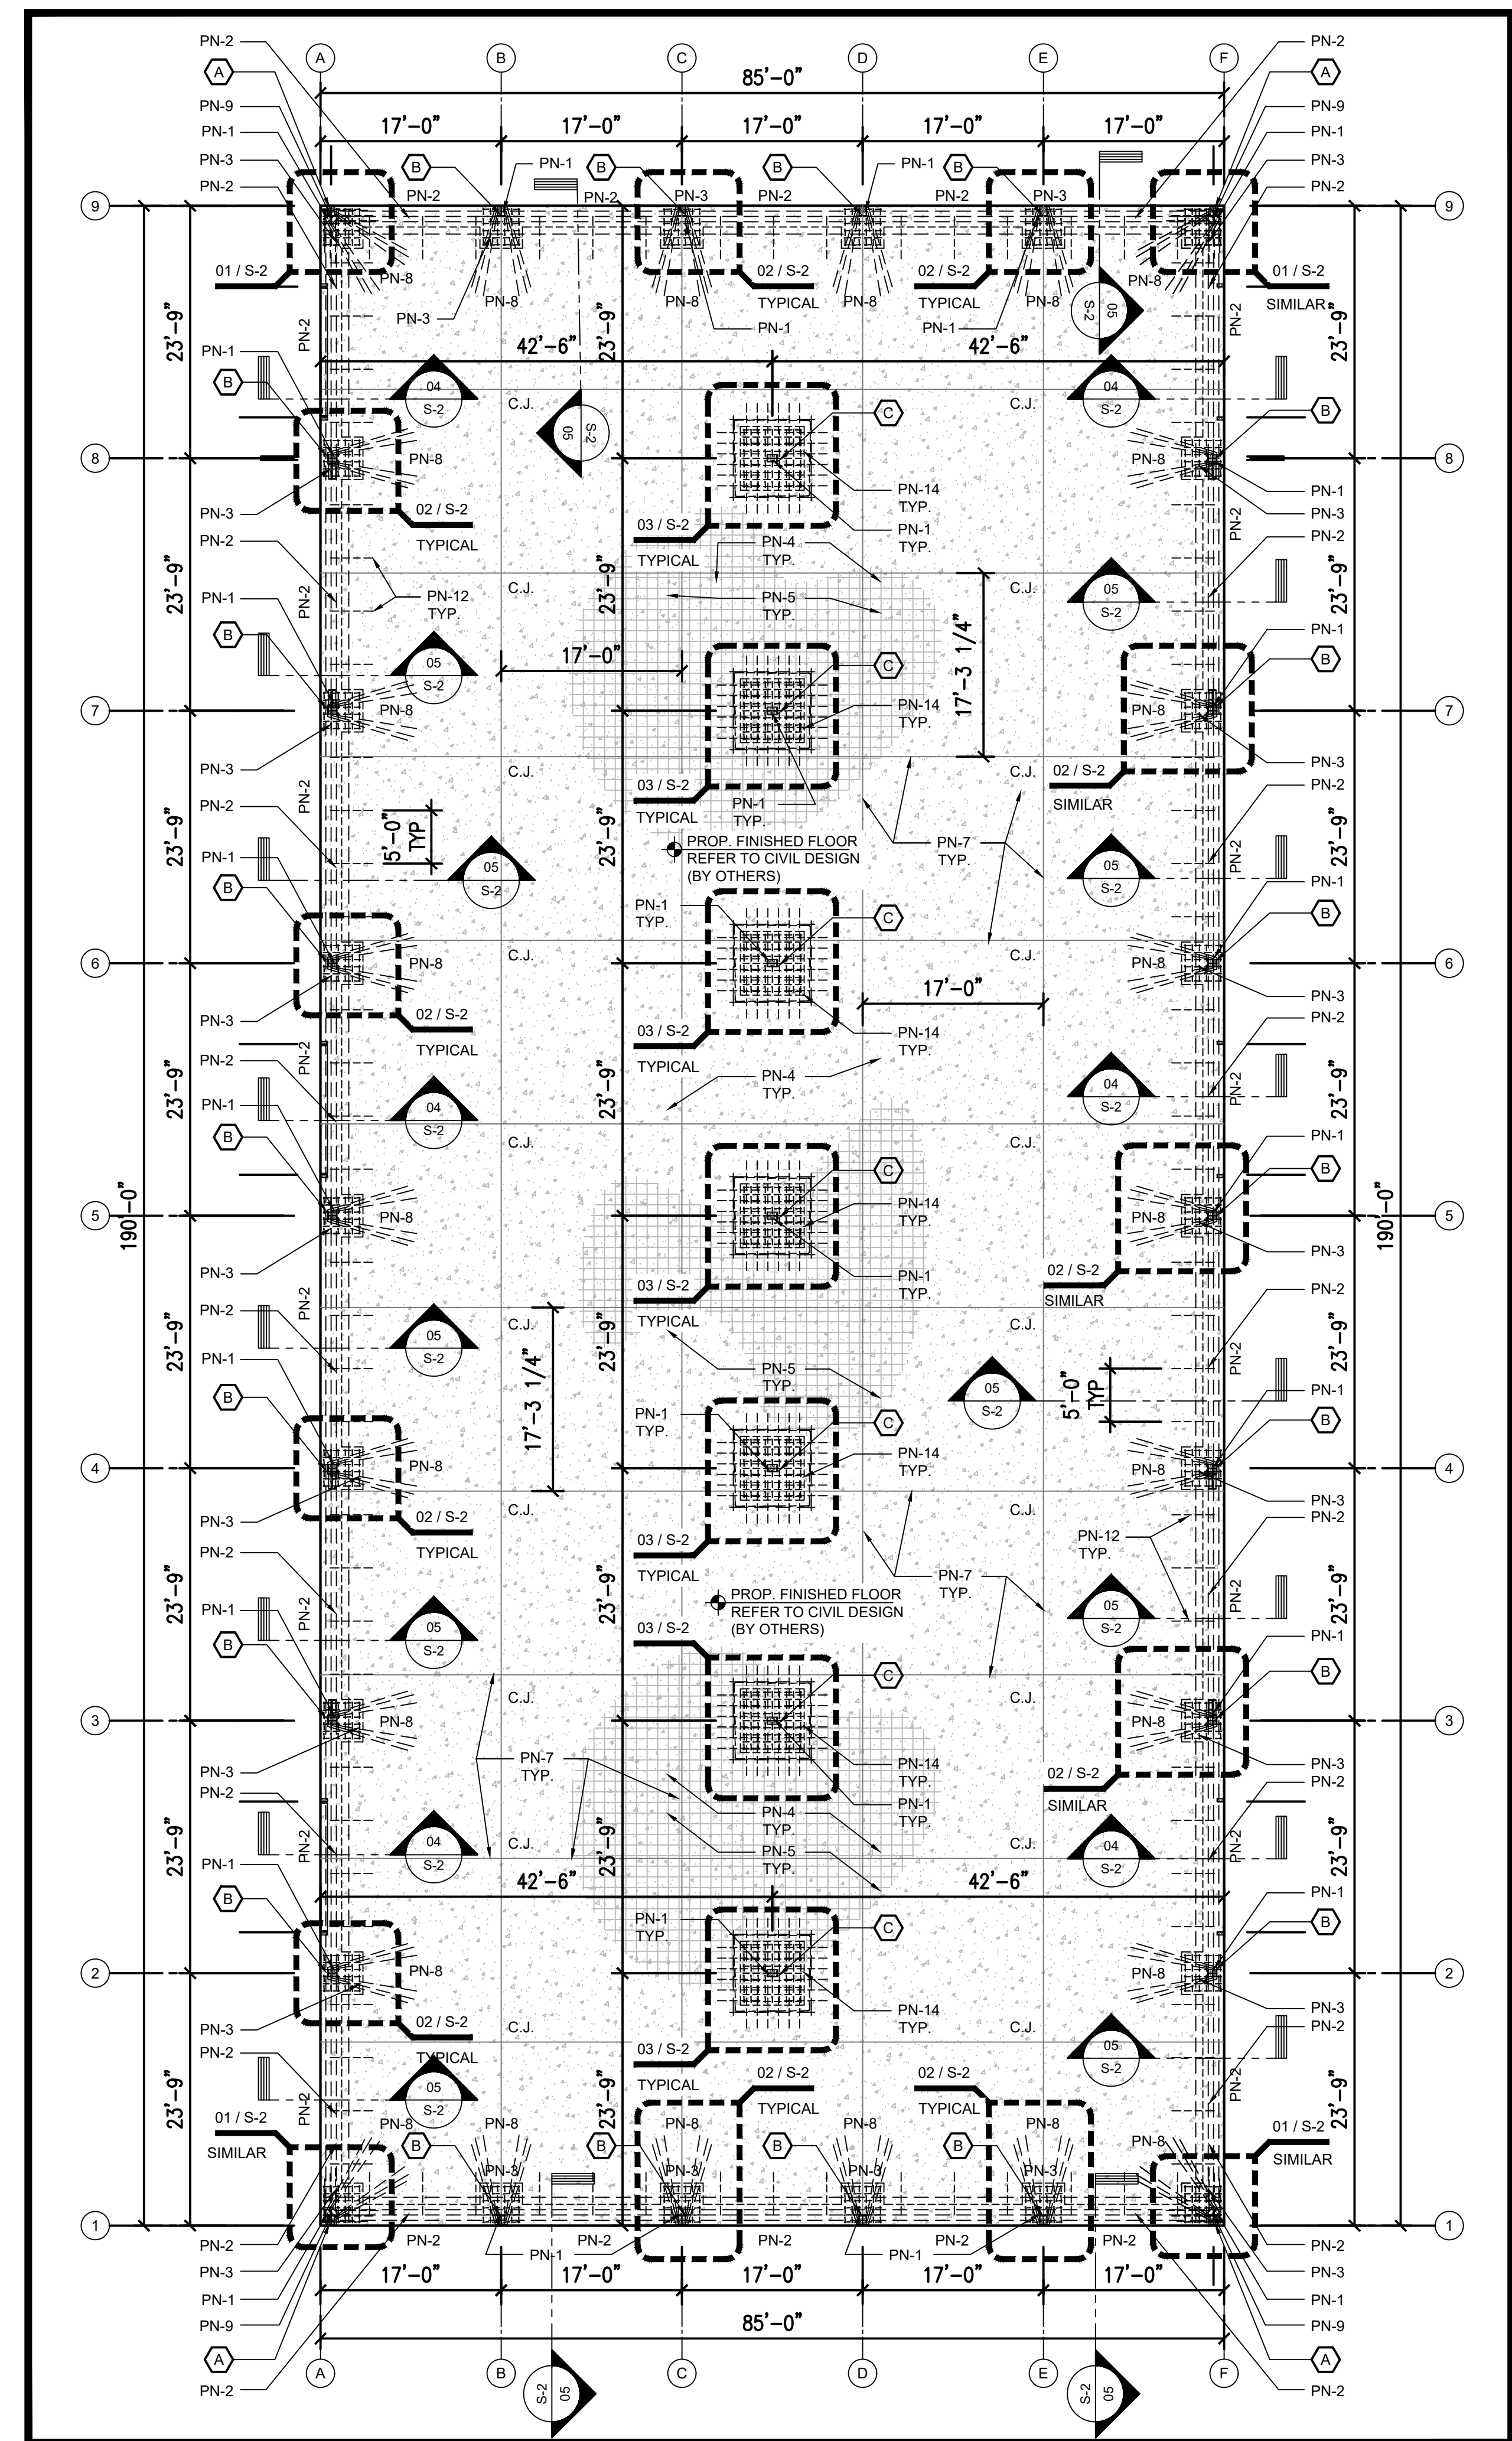

SCALE: 1" = 20'-0"



