


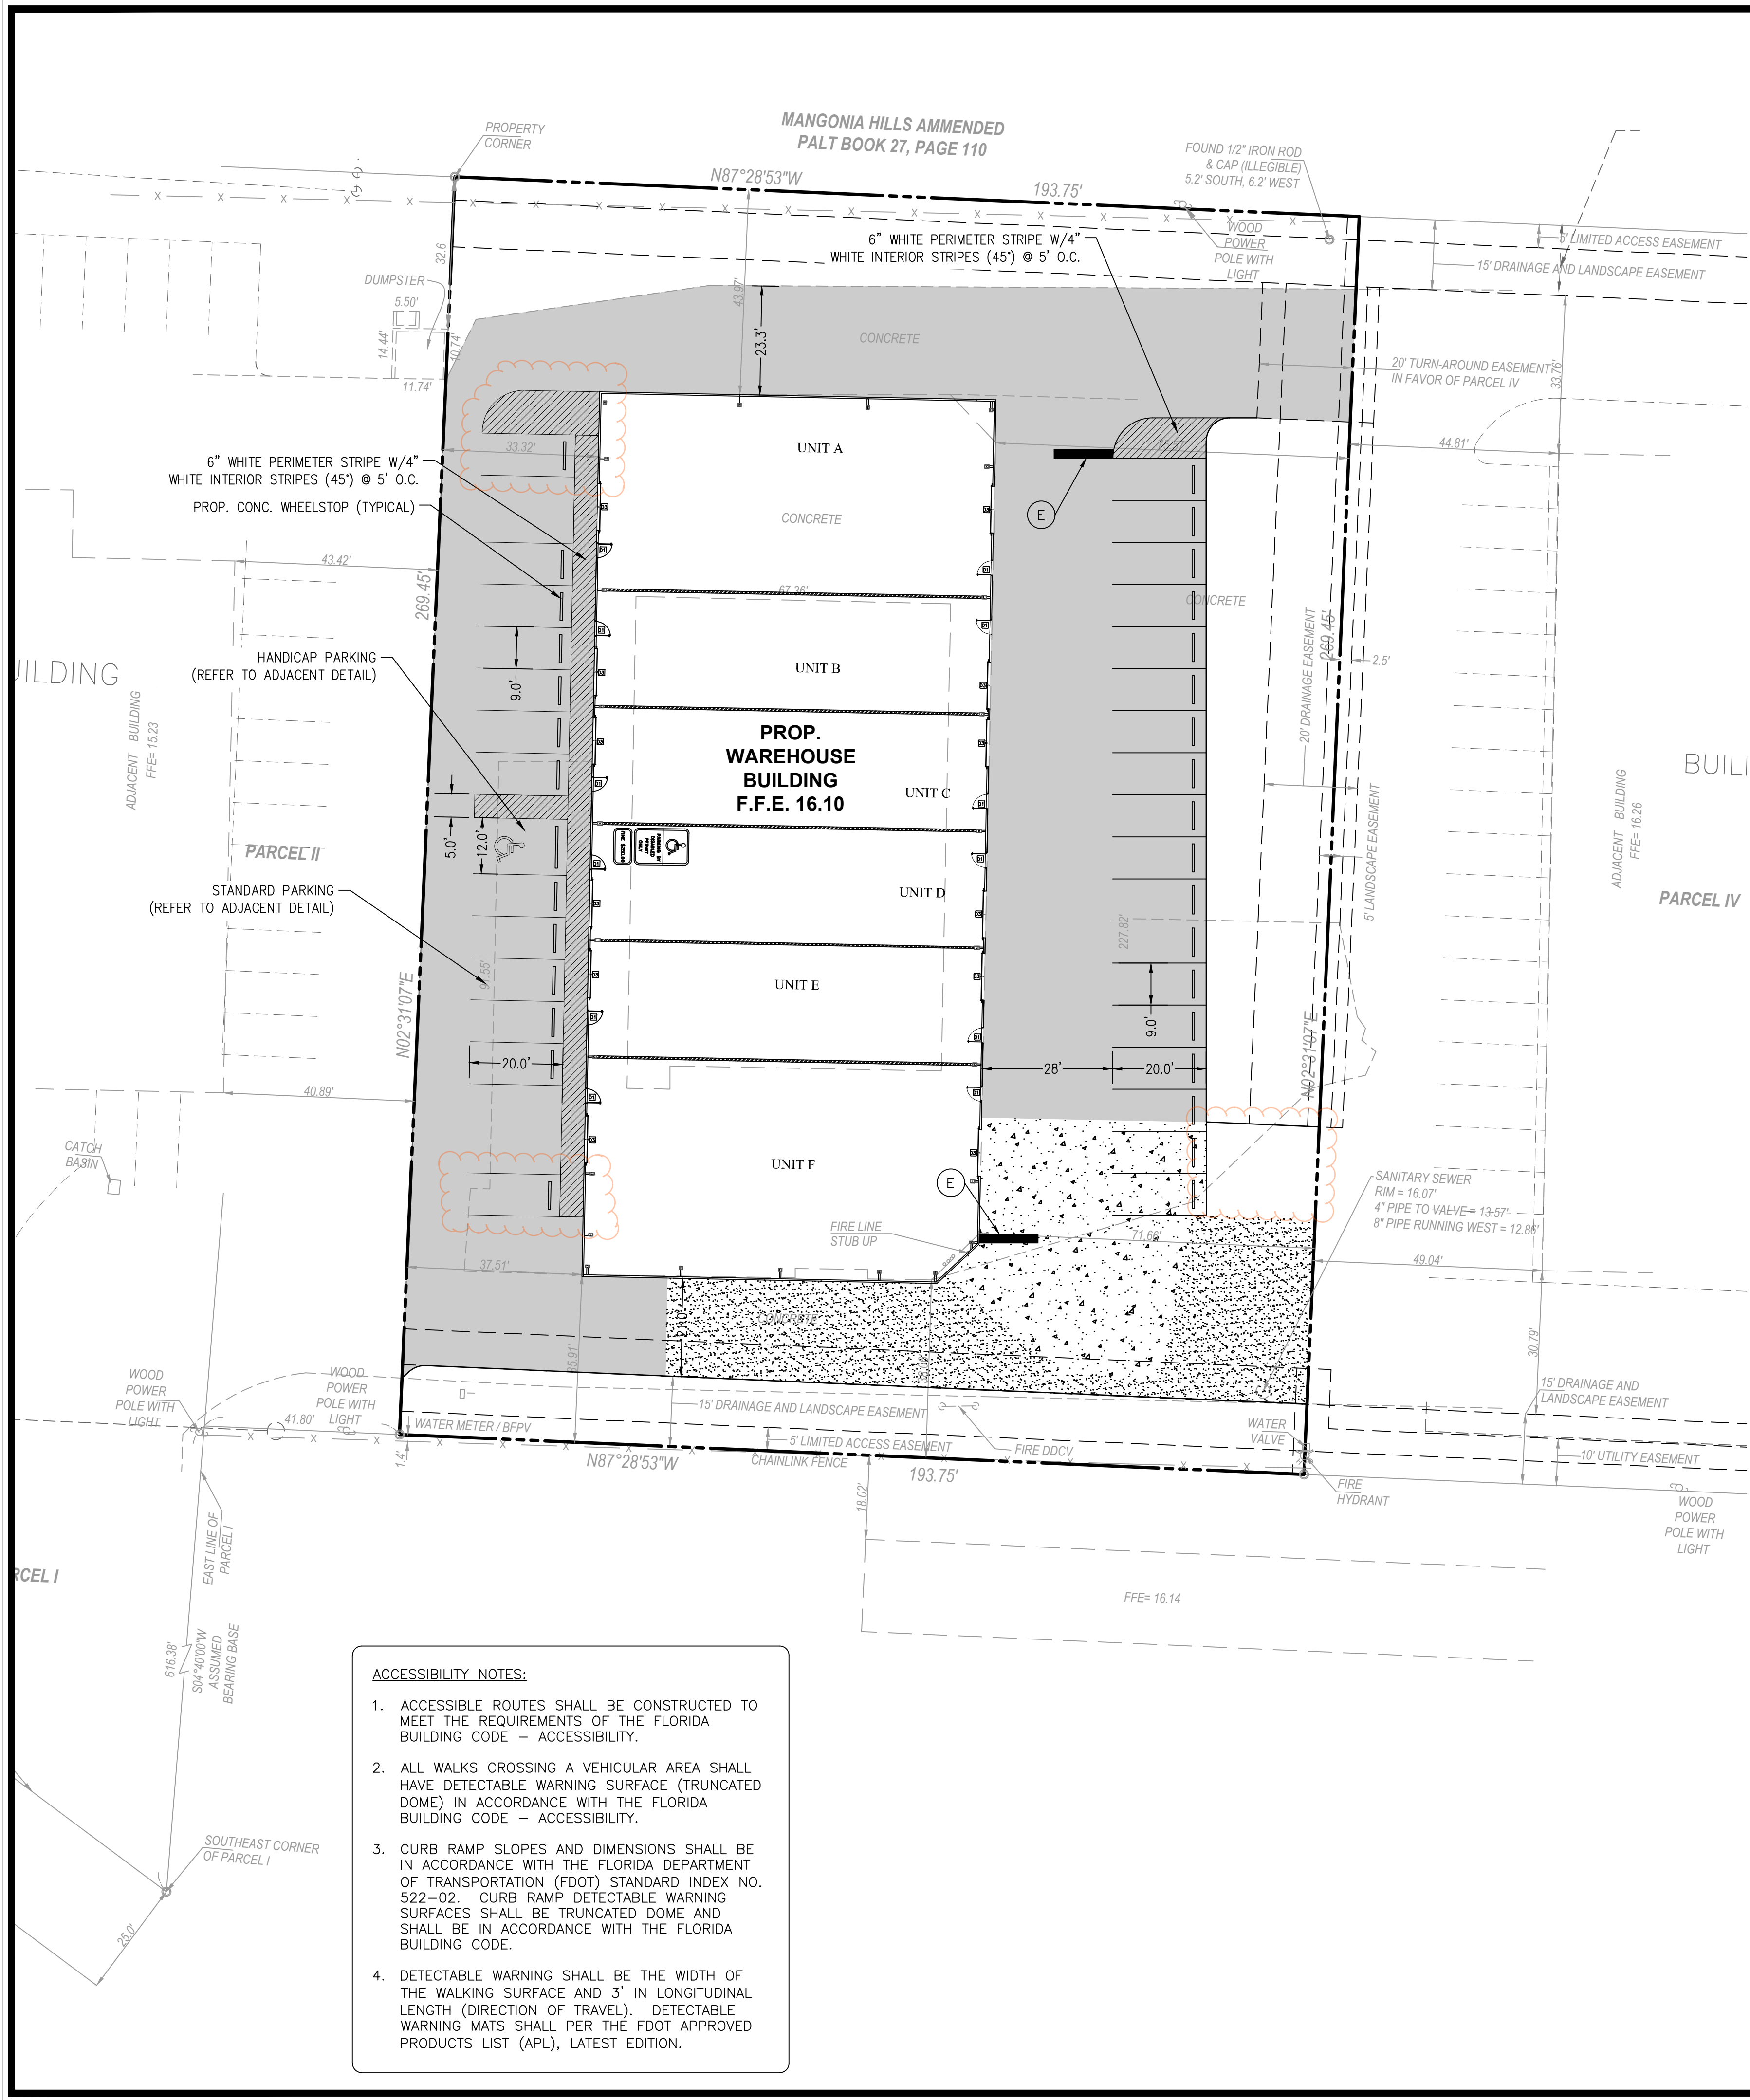

STRIPING LEGEND

6" SOLID WHITE STRIPE	(A)
8" SOLID WHITE STRIPE	(B)
12" SOLID WHITE STRIPE	(C)
18" SOLID WHITE STRIPE	(D)
24" SOLID WHITE STRIPE	(E)
6" SKIP WHITE (10'-30')	(F)
6" SKIP WHITE (6'-10')	(G)
6" SKIP WHITE (2'-4')	(H)
6" SOLID YELLOW	(I)
18" SOLID YELLOW	(J)
6" DOUBLE YELLOW	(K)
6" SKIP YELLOW (10'-30')	(L)
6" SKIP YELLOW (6'-10')	(M)
6" SKIP YELLOW (2'-4')	(N)
RPM BI-DIRECTIONAL AMBER/AMBER	(P)
FDP WHITE	(R)
FDP YELLOW	(S)
RPM BI-DIRECTIONAL WHITE/RED	(T)
RPM BI-DIRECTIONAL RED/YELLOW	(U)

(A)
(B)
(C)
(D)
(E)
(F)
(G)
(H)
(I)
(J)
(K)
(L)
(M)
(N)
(P)
(R)
(S)
(T)
(U)


LEGEND

PROP. SIGN	(CR-X)
CURB RAMP PER FDOT INDEX NO. 522-002	
PROP. CONCRETE PAVEMENT	
EXIST. CONC. PAVEMENT	
MILLING & RESURFACING	

CURBING LEGEND

TYPE "D" CURB	(1)
TYPE "F" CURB & GUTTER	(2)
2' VALLEY GUTTER	(3)
12" HEADER CURB	(4)
DETECTABLE WARNING (PER FDOT 522-02)	(5)
TYPE "B" CURB	(6)

- NOTES:
- PAVEMENT MARKINGS & SIGNAGE SHALL BE IN ACCORDANCE WITH THE MANUAL ON UNIFORM TRAFFIC CONTROL DEVICES FOR STREETS AND HIGHWAYS (MUTCD) AND TOWN OF MANGONIA PARK LAND DEVELOPMENT CODE.
 - PARKING STALL STRIPING SHALL BE TRAFFIC PAINT; ALL OTHER STRIPING SHALL BE THERMOPLASTIC.
 - CURB RAMPS SHALL BE CONSTRUCTED IN ACCORDANCE WITH FDOT STANDARD INDEX FOR ROAD CONSTRUCTION NO. 522-002.

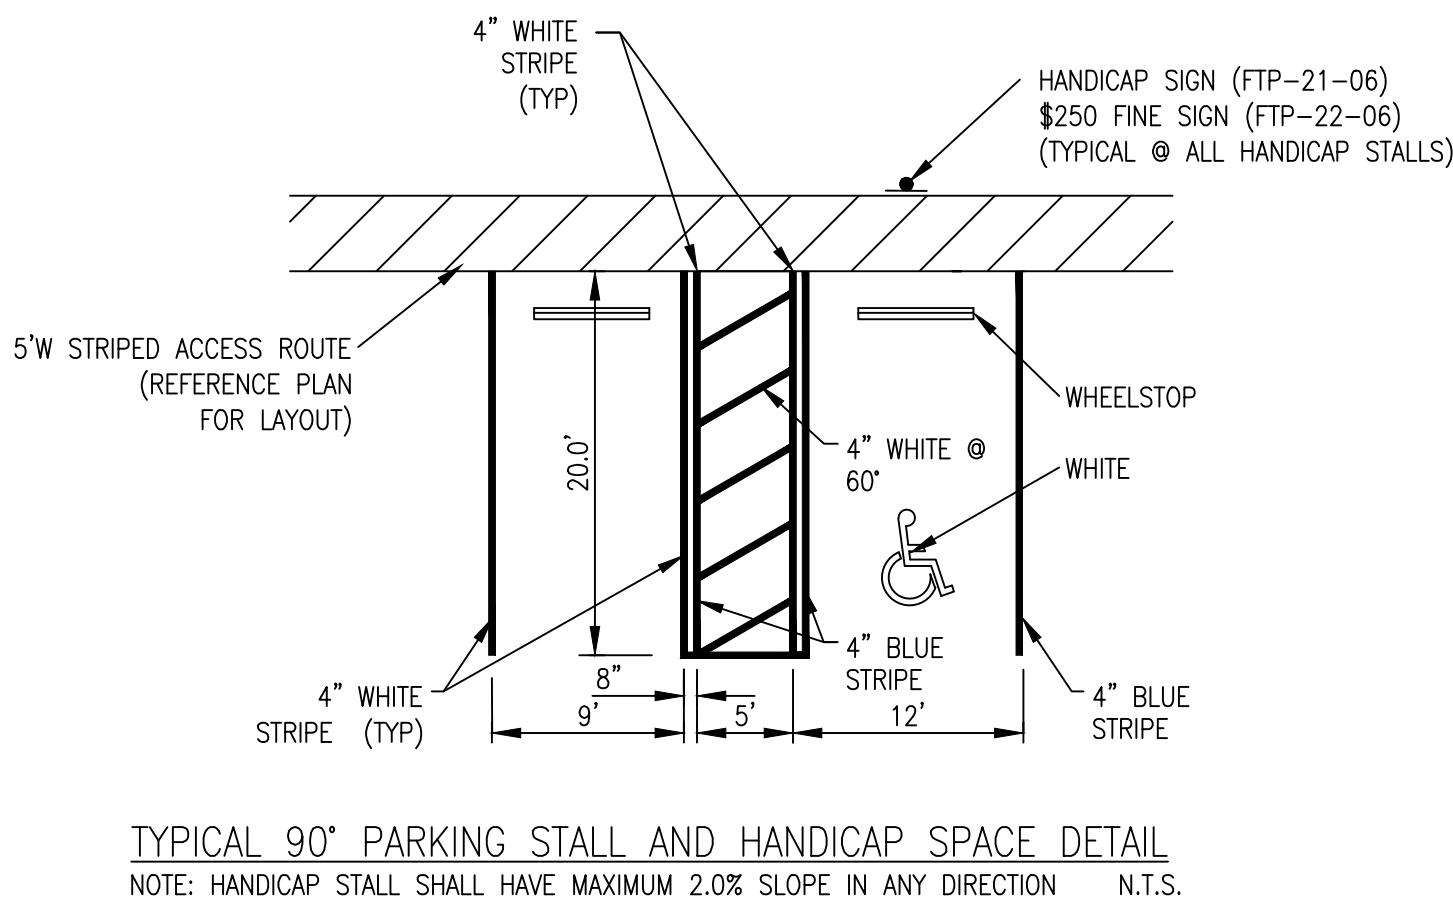


ALL ELEVATIONS REFER TO NORTH AMERICAN VERTICAL DATUM OF 1988 (NAVD 88). TO CONVERT TO NGVD 29 DATUM, ADD 1.54' TO NAVD ELEVATIONS.

NOTE: THESE PLANS ARE PRELIMINARY AND SHOULD NOT BE USED FOR CONSTRUCTION OR BIDDING/CONTRACTUAL PURPOSES UNTIL ALL PERMITS ARE ISSUED.



McLeod • McCarthy
& Associates, P.A.
Civil Engineers

The Forum III
1319 Mangonia Park Blvd, Ste. 901
Mangonia Park, FL 33401
P: 561.689.9500
F: 561.689.8080
www.mcleodmccarthy.com

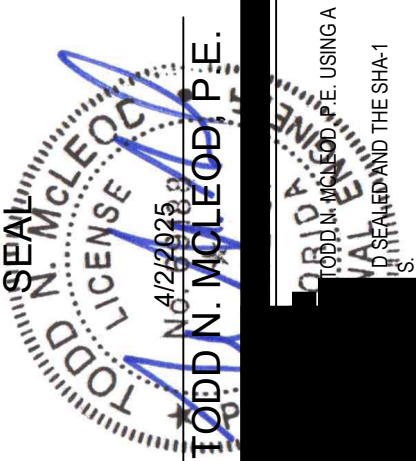

FIELD: DRAWN: P. Saffold
DESIGNED: TMM
APPROVED: TMM
PROJECT #21-030

NO.	DATE	REVISIONS
3	4/2/2025	STRIPING REV PER OWNER

GEOMETRIC, SIGNING, & MARKING PLAN
1319 MANGONIA PARK WAREHOUSE
MANGONIA PARK, FLORIDA

TOWN RESUBMITTAL
DATE: 8/1/2024

SHEET
C2.2
OF 13