

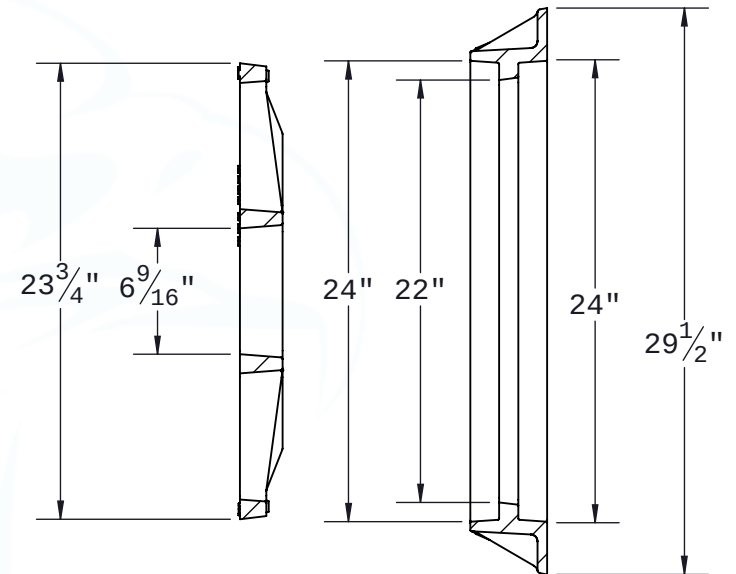


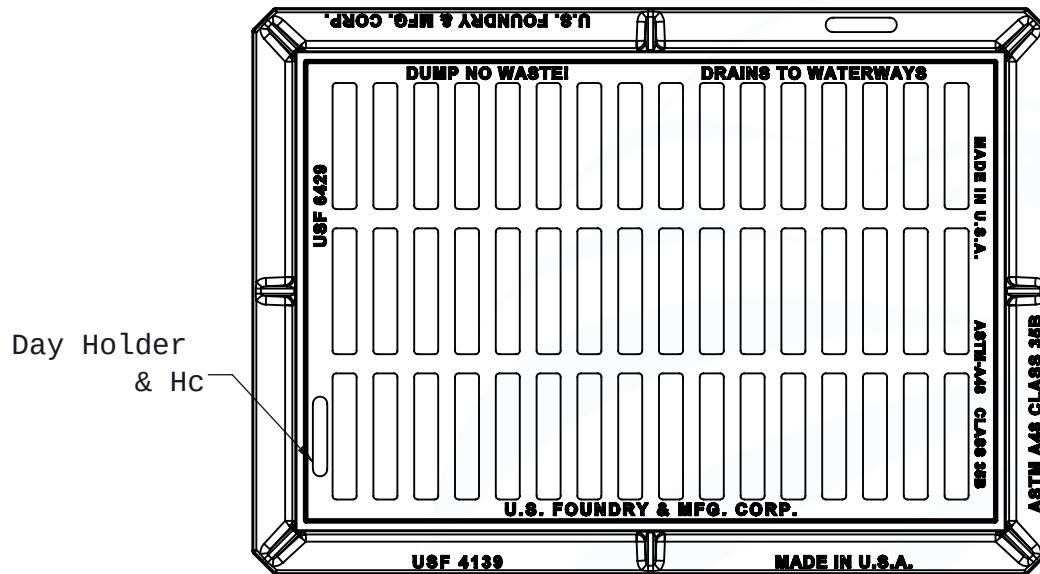


Approved by McLeod-McCarthy & Associates.
Engineer's review is for general conformance.
Approval does not relieve the Contractor from
compliance with all requirements of Construction
Documents

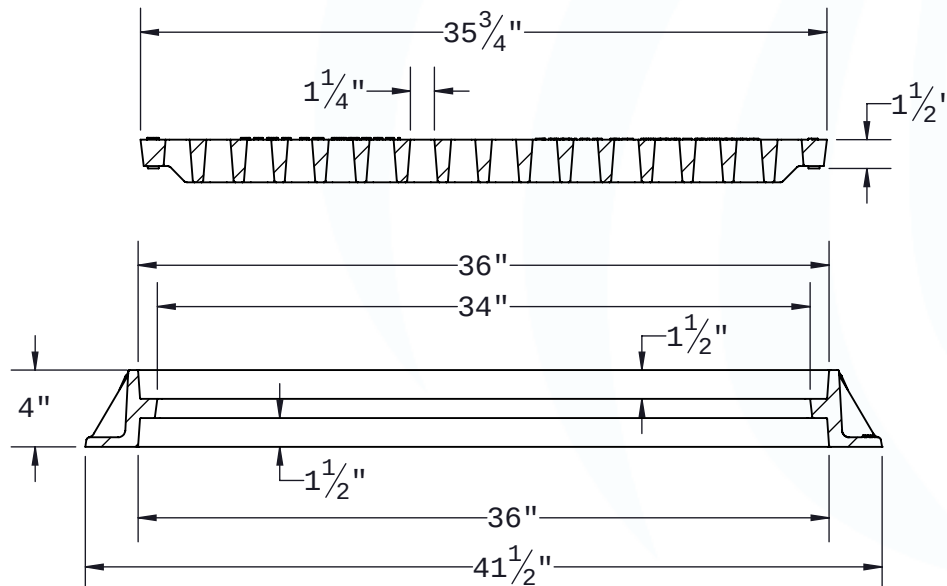

USF 4139 Frame & 6429 Grate

ITEM	BAAN #	MATERIAL:
Frame	8030032	Gray Cast Iron
Grate	8070191	ASTM-A48 Class 35B
		LOAD CLASSIFICATION:
		AASHTO M306
Assembly	8040048	FLOW AREA:
REV 0	REV DATE	REV BY
		DRAWN DATE 2/3/1992

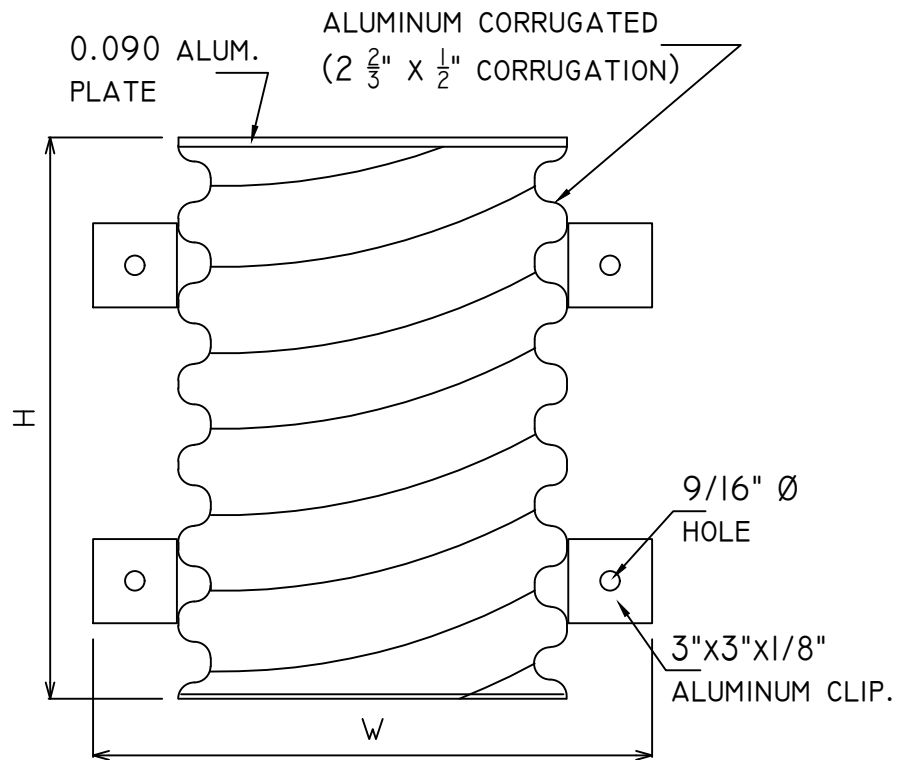


DIMENSIONS					
PIPE Ø	D _b	GAUGE	HEIGHT (H)	W	DEPTH (P)
15"	24"	16	27"	30"	12.5

NOTE: | - ALL DIMENSIONS ARE IN INCHES.

S-101
S-102
S-103
S-104

3"x $\frac{1}{2}$ " NEOPRENE GASKET ON
ALL SURFACE BETWEEN
BAFFLE & CATCH BASIN

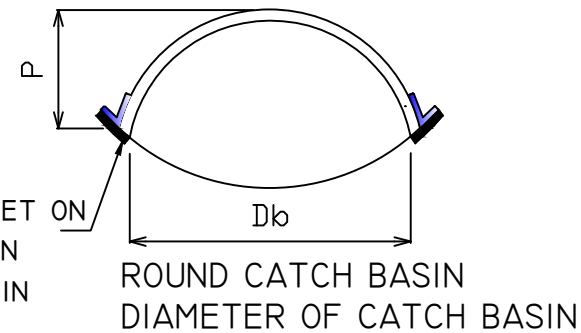

438 NW 10 TH AVE
Homestead FL 33030
PH:305-242-8888
fax:305-242-6200

DATE: 10/31/24

ALUMINUM BAFFLE ROUND STRUCTURE

JOB NAME:

MANGONIA PARK WAREHOUSE

QTY : 6


CUSTOMER:

SHWETA INVESTMENT LLC

DWG : RI


STR.No.

REBAR	W.W.MESH	CONCRETE	COMPONENT:	WALL	TOP.SLAB O.D DIMENS	BOT SLAB O.D DIMENS		WEIGHT (Lbs)	YD ³
GRADE 60	70 KSI	4000PSI@28DAYS		6"	54"Ø	54"Ø	BASE	6,690	1.67
							RISER	NA	NA
							TOP SLAB	978	0.24
							TOTAL	7,668	1.92

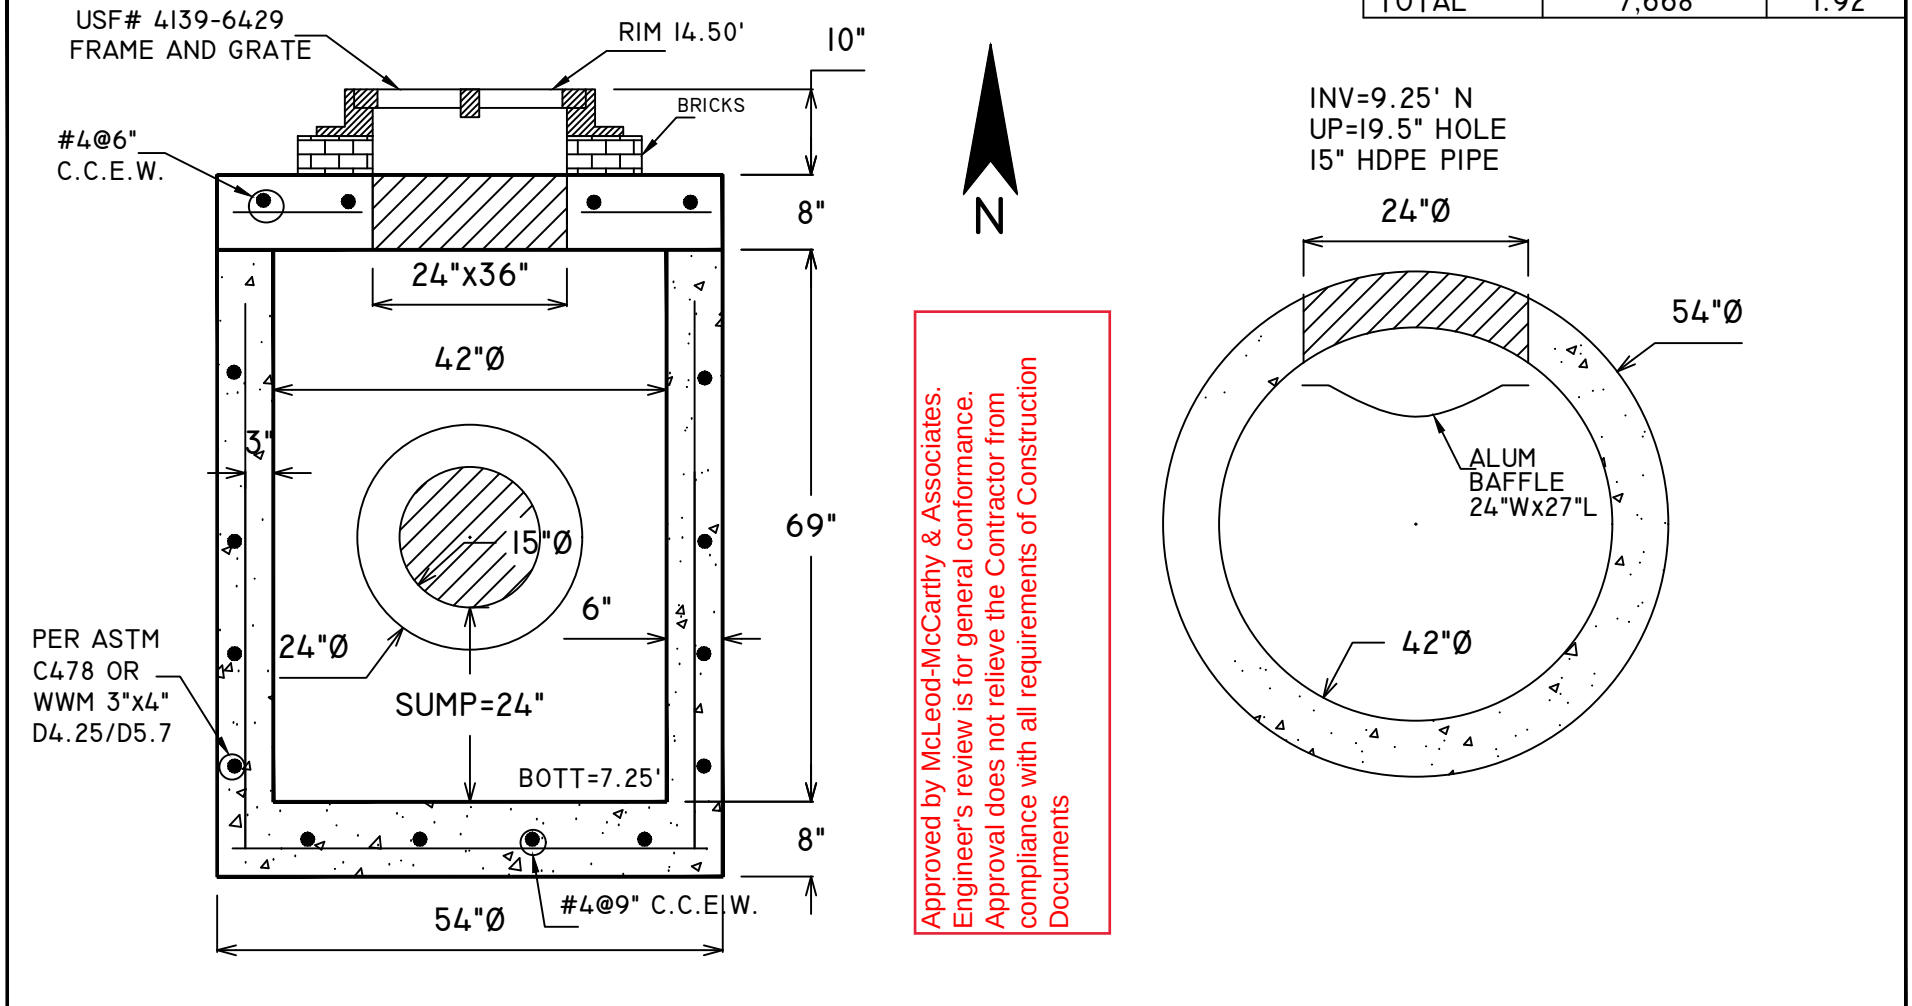


  PH:305-242-8888 FAX:305-242-6200	DATE: 10/31/24		TYPE P 42" RD, CB STR.	INV: 9.25'(N)
	JOB NAME:	MANGONIA PARK WAREHOUSE		SUMP: 24"
	CUSTOMER:	SHWETA INVESTMENT LLC		DWG : RI
	CASTING:	USF# 4139-6429 FRAME AND GRATE		STR.No. S-101
	PLAN DATE: 01/25/22		SHEET: C2.1	

REBAR	W.W.MESH	CONCRETE	COMPONENT:	WALL	TOP.SLAB O.D DIMENS	BOT SLAB O.D DIMENS		WEIGHT (Lbs)	YD ³
GRADE 60	70 KSI	4000PSI@28DAYS		8"	64"Ø	76"Ø	BASE	10,816	2.70
							RISER	NA	NA
							TOP SLAB	1,613	0.40
							TOTAL	12,430	3.11

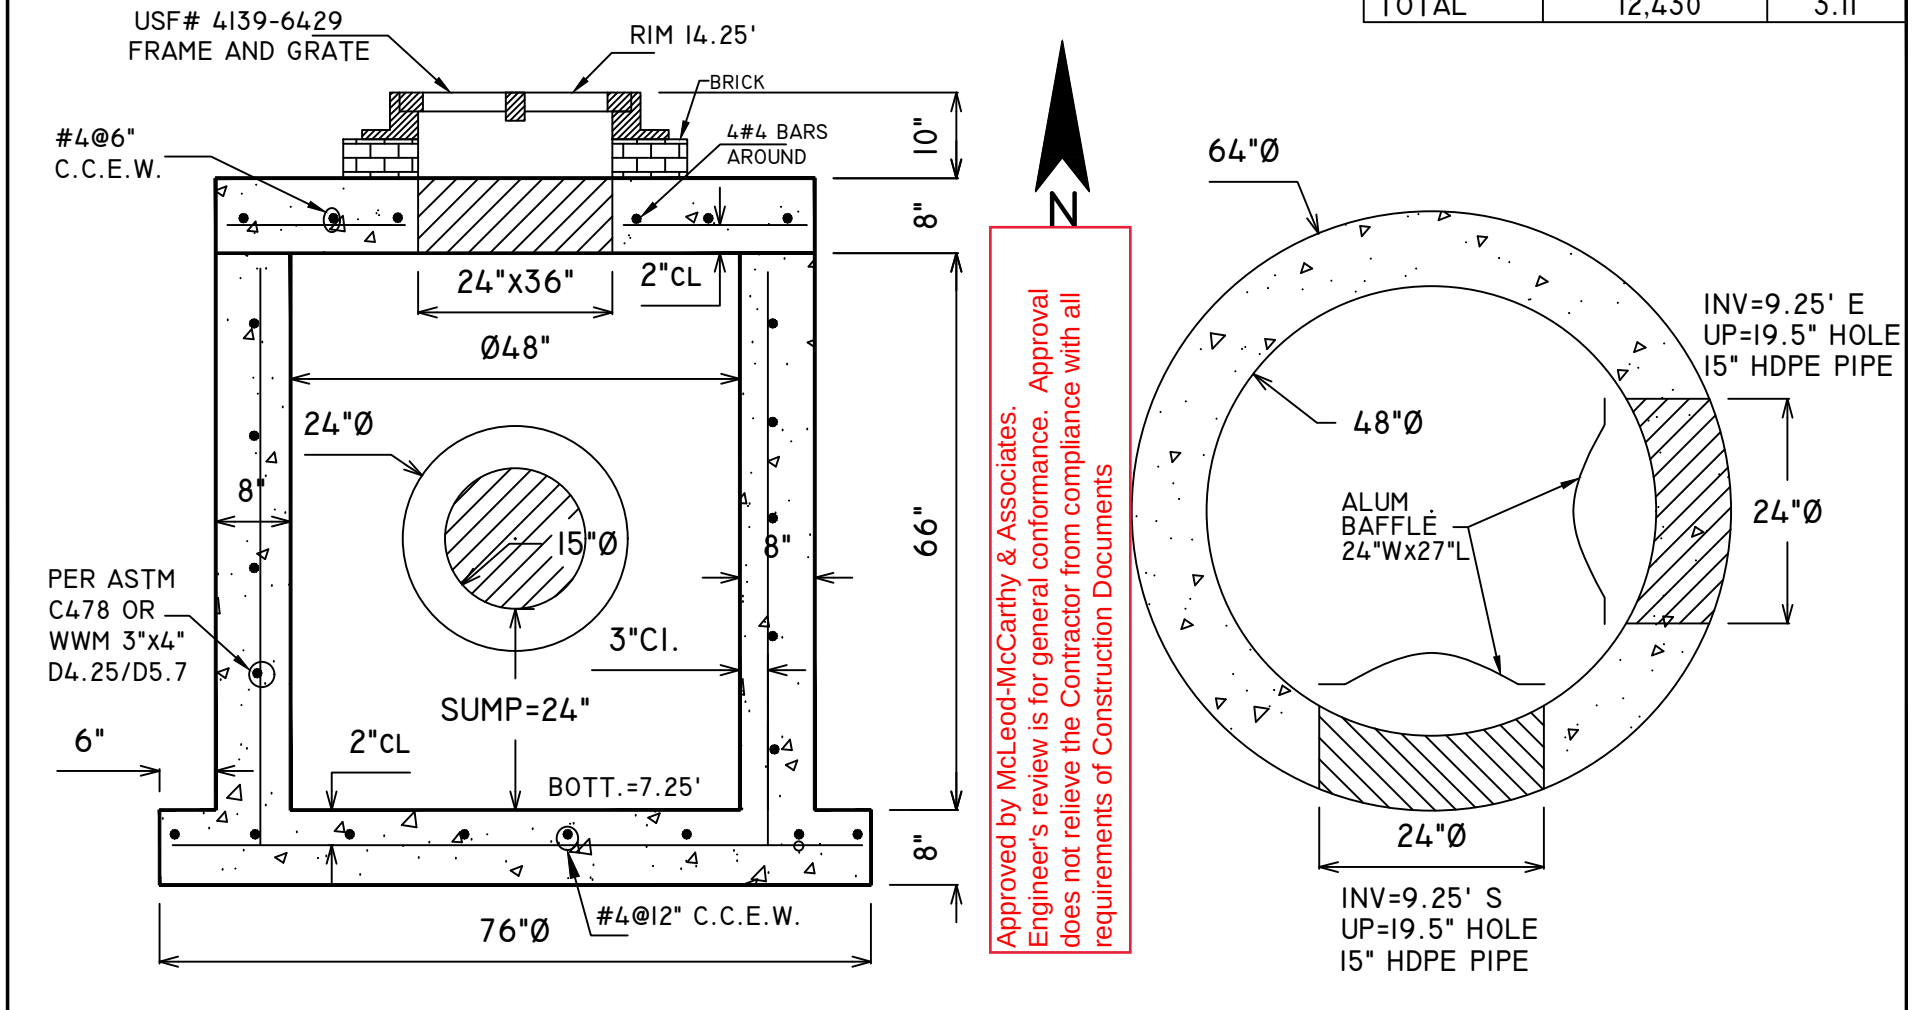

 PH:305-242-8888 FAX:305-242-6200	DATE: 10/31/24	TYPE P CATCH BASIN - 48" ROUND STR.	INV: 9.25'(E/S)
	JOB NAME:	MANGONIA PARK WAREHOUSE	SUMP: 24"
	CUSTOMER:	SHWETA INVESTMENT LLC	DWG: RI
	CASTING:	USF# 4139-6429 FRAME AND GRATE	
	PLAN DATE: 01/25/22	SHEET: C2.1	STR.No. S-102

REBAR	W.W.MESH	CONCRETE	COMPONENT:	WALL	TOP.SLAB O.D DIMENS	BOT SLAB O.D DIMENS		WEIGHT (Lbs)	YD ³
GRADE 60	70 KSI	4000PSI@28DAYS		8"	64"Ø	76"Ø	BASE	10,816	2.70
							RISER	NA	NA
							TOP SLAB	1,613	0.40
							TOTAL	12,430	3.11

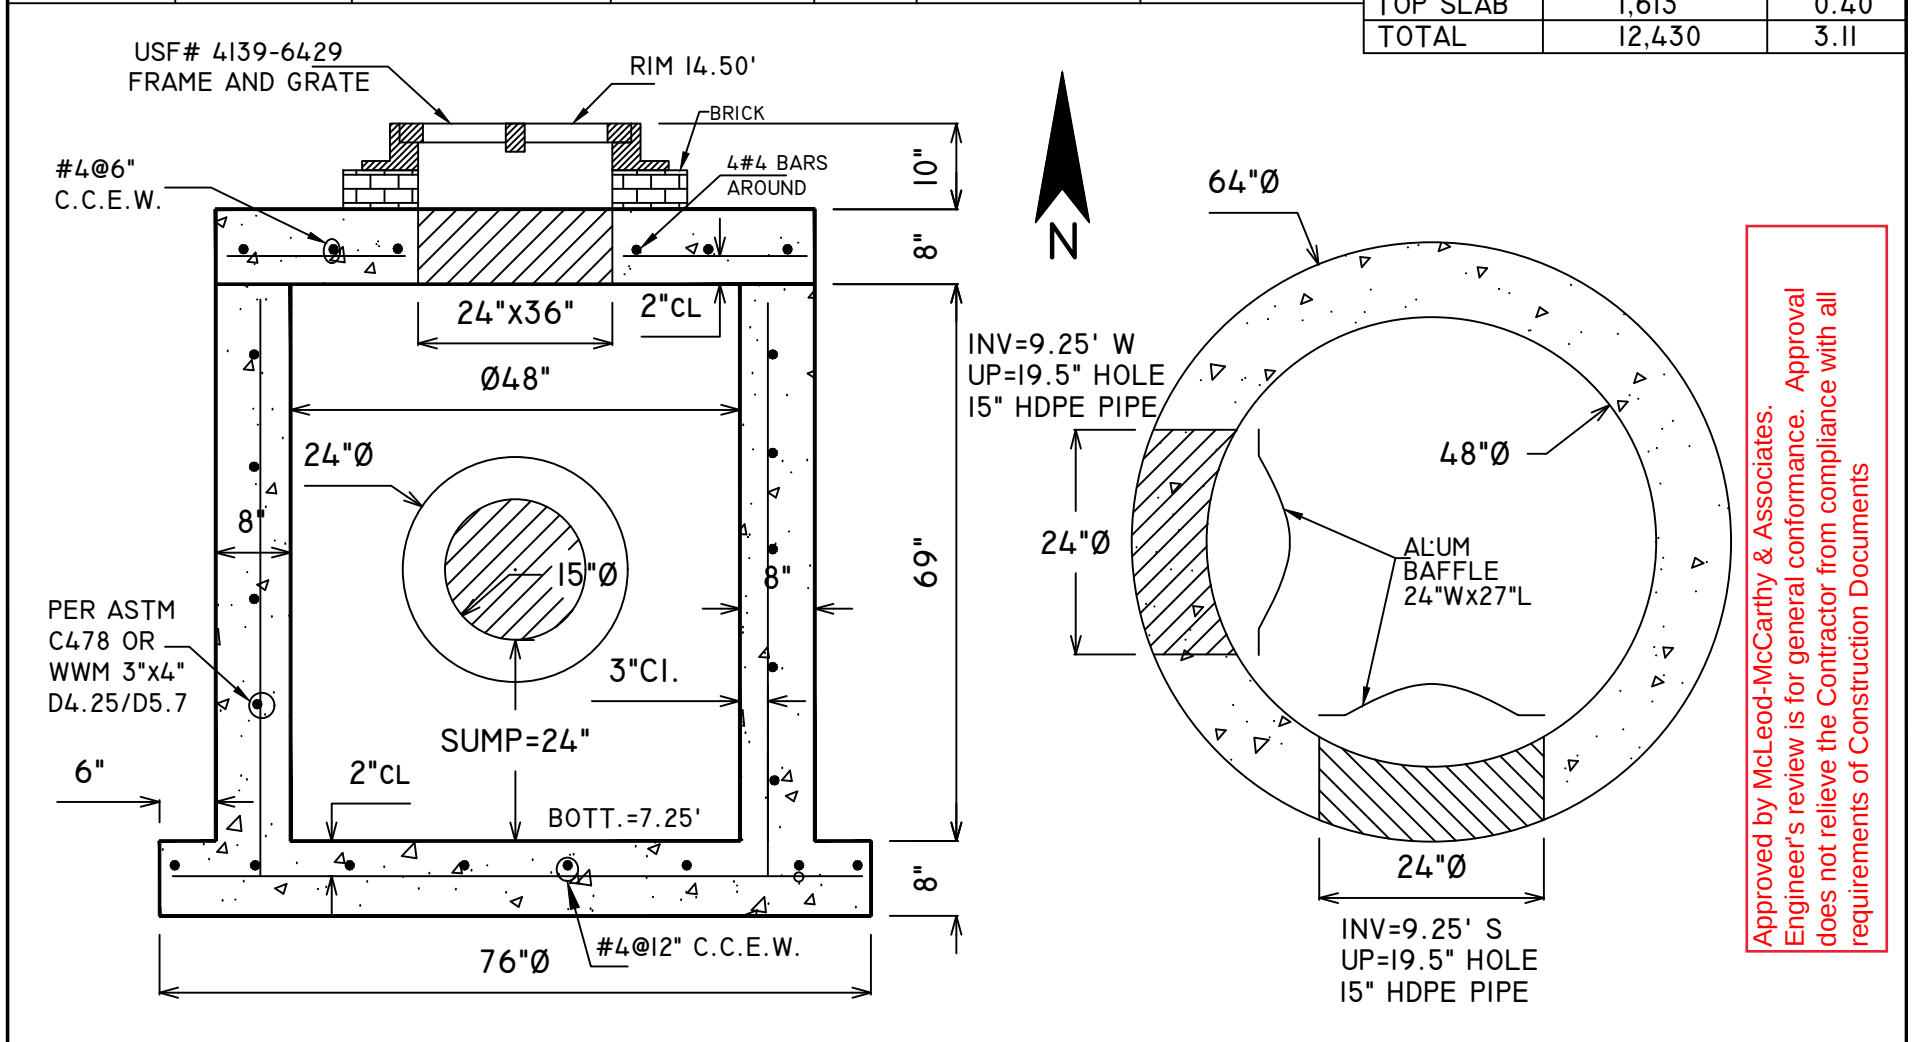

Approved by McLeod-McCarthy & Associates.
Engineer's review is for general conformance. Approval
does not relieve the Contractor from compliance with all
requirements of Construction Documents



PH:305-242-8888
FAX:305-242-6200

DATE: 10/31/24

TYPE P CATCH BASIN - 48" ROUND STR.

INV: 9.25'(W/S)

JOB NAME:

MANGONIA PARK WAREHOUSE

SUMP: 24"

CUSTOMER:

SHWETA INVESTMENT LLC

DWG: RI

CASTING:


USF# 4139-6429 FRAME AND GRATE

STR.No. S-I03

PLAN DATE: 01/25/22

SHEET: C2.1

REBAR	W.W.MESH	CONCRETE	COMPONENT:	WALL	TOP.SLAB O.D DIMENS	BOT SLAB O.D DIMENS		WEIGHT (Lbs)	YD ³
GRADE 60	70 KSI	4000PSI@28DAYS		6"	54"Ø	54"Ø	BASE	6,690	1.67
							RISER	NA	NA
							TOP SLAB	978	0.24
							TOTAL	7,668	1.92

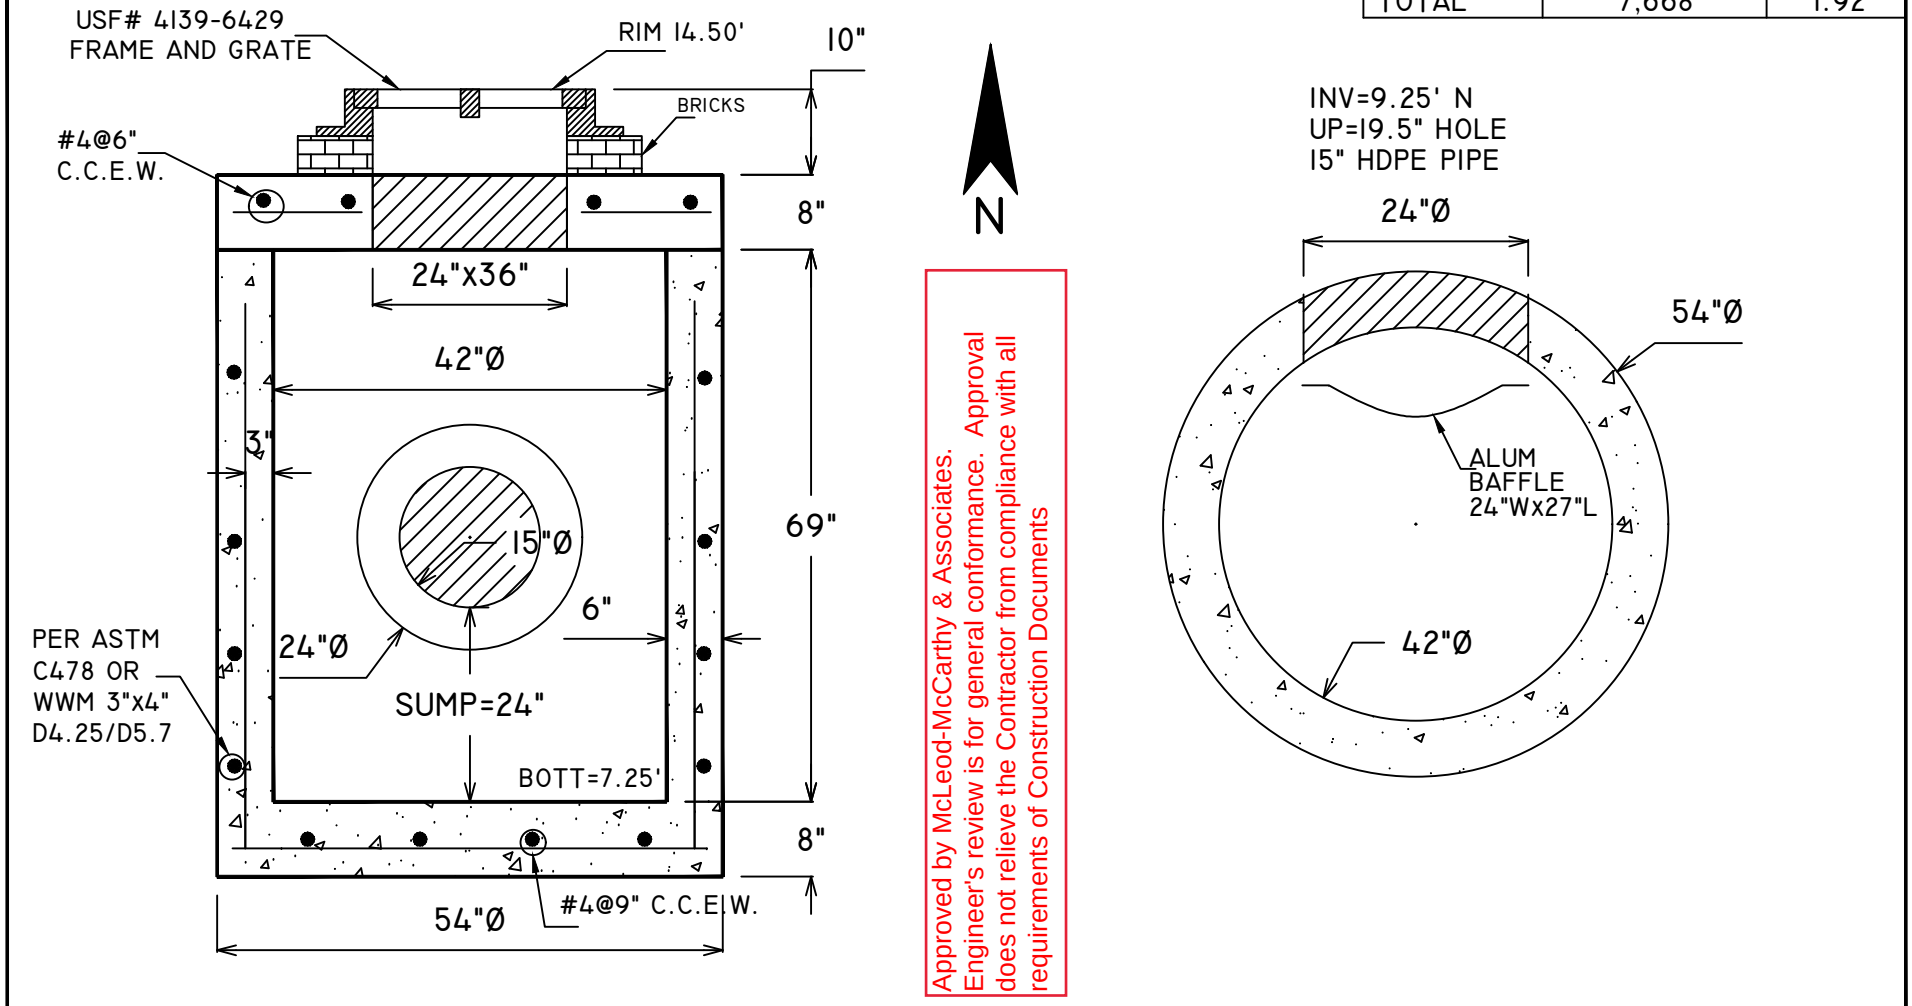

 PH:305-242-8888 FAX:305-242-6200	DATE: 10/31/24	TYPE P 42" RD, CB STR.	INV: 9.25'(N)
	JOB NAME:	MANGONIA PARK WAREHOUSE	SUMP: 24"
	CUSTOMER:	SHWETA INVESTMENT LLC	DWG: RI
	CASTING:	USF# 4139-6429 FRAME AND GRATE	STR.No. S-104
	PLAN DATE: 01/25/22	SHEET: C2.1	